


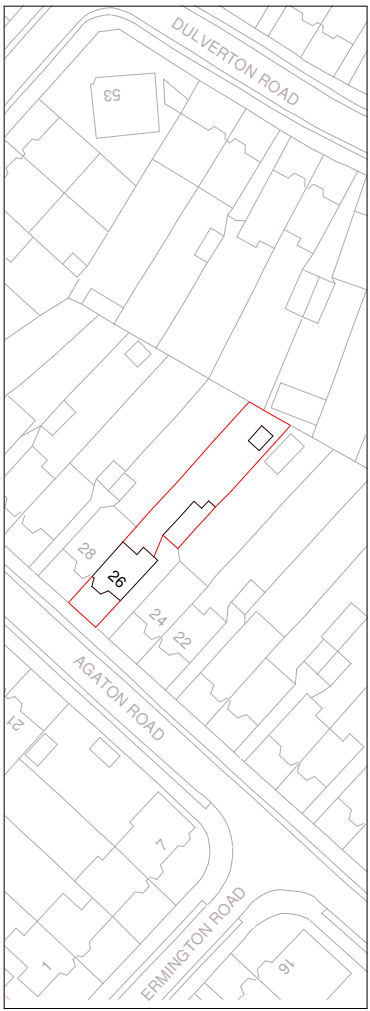
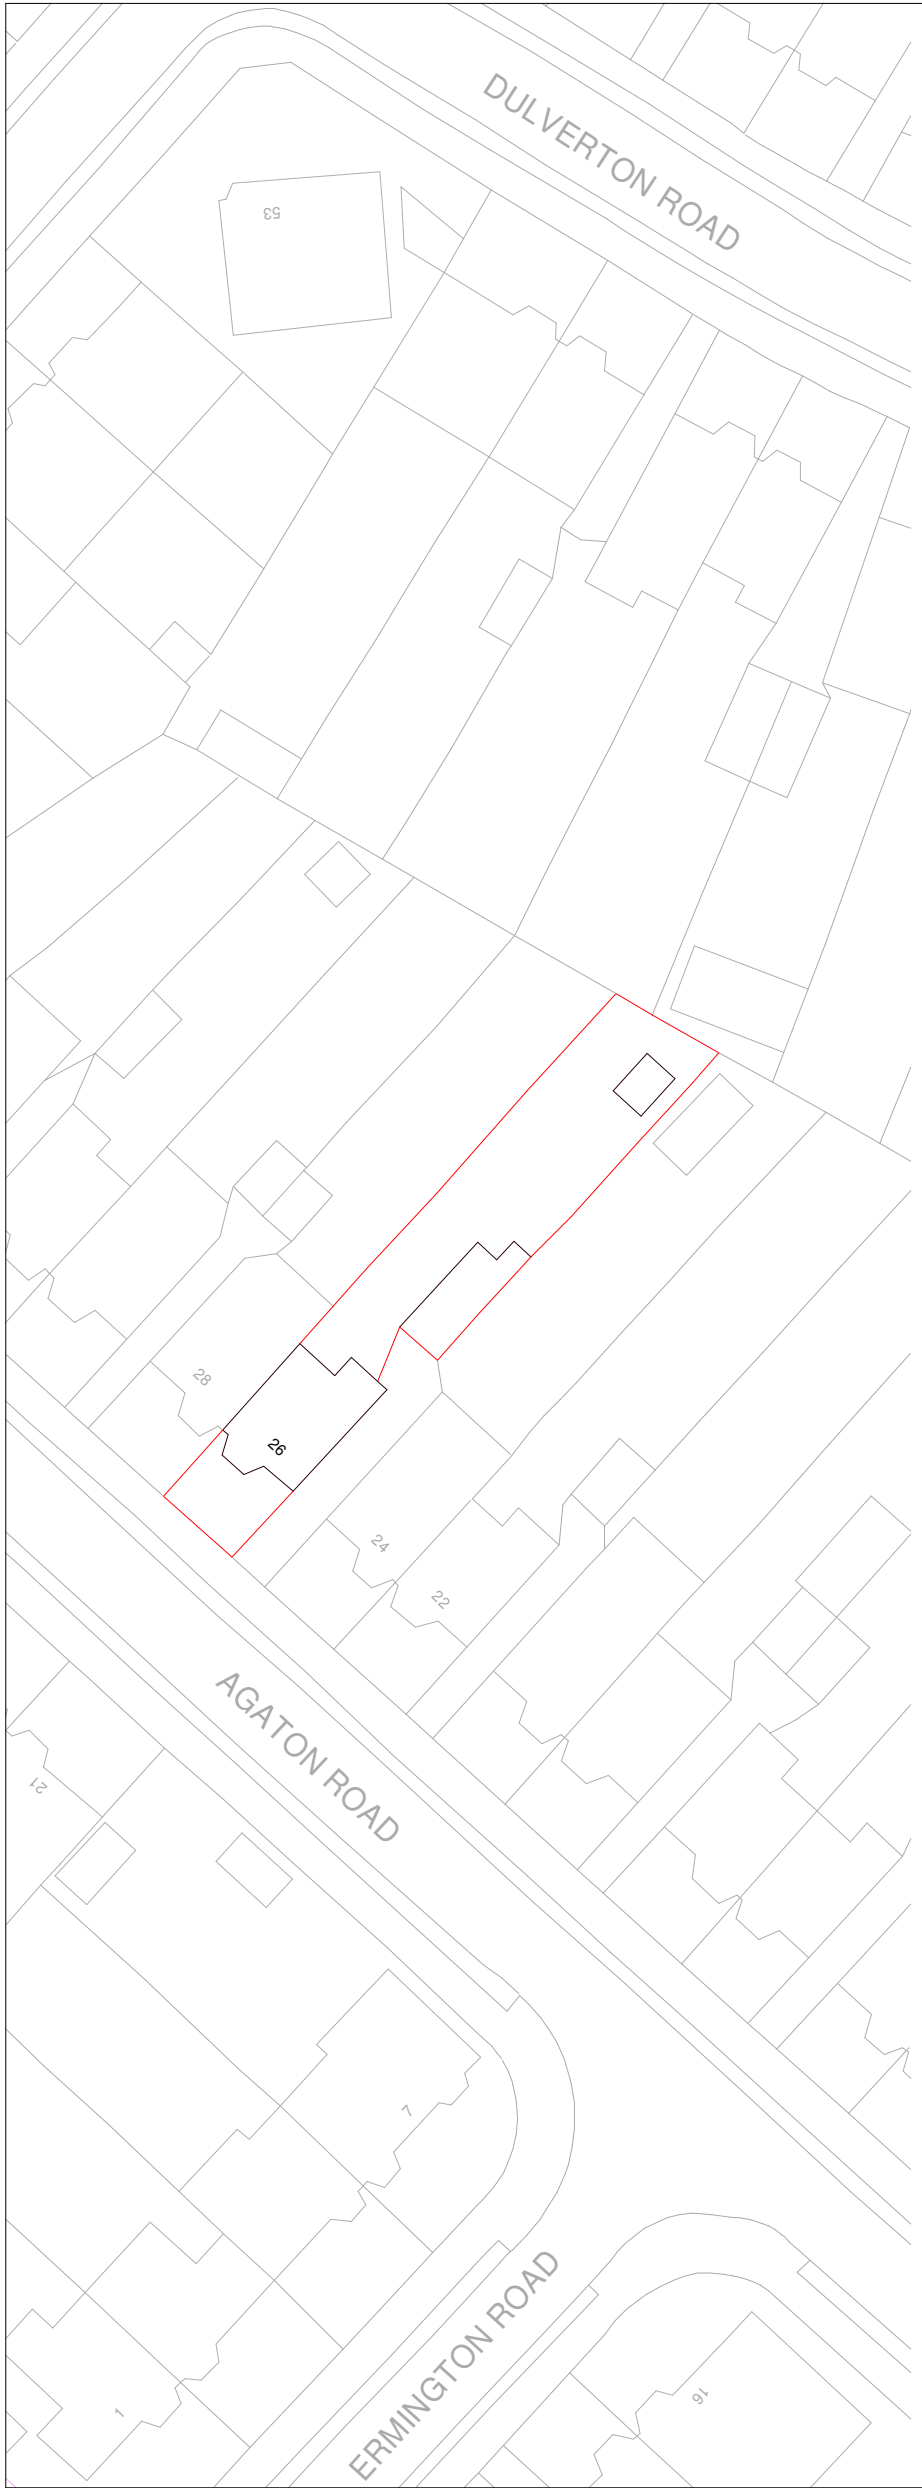


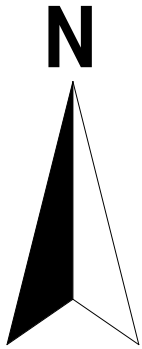


Location Plan
1 : 1250

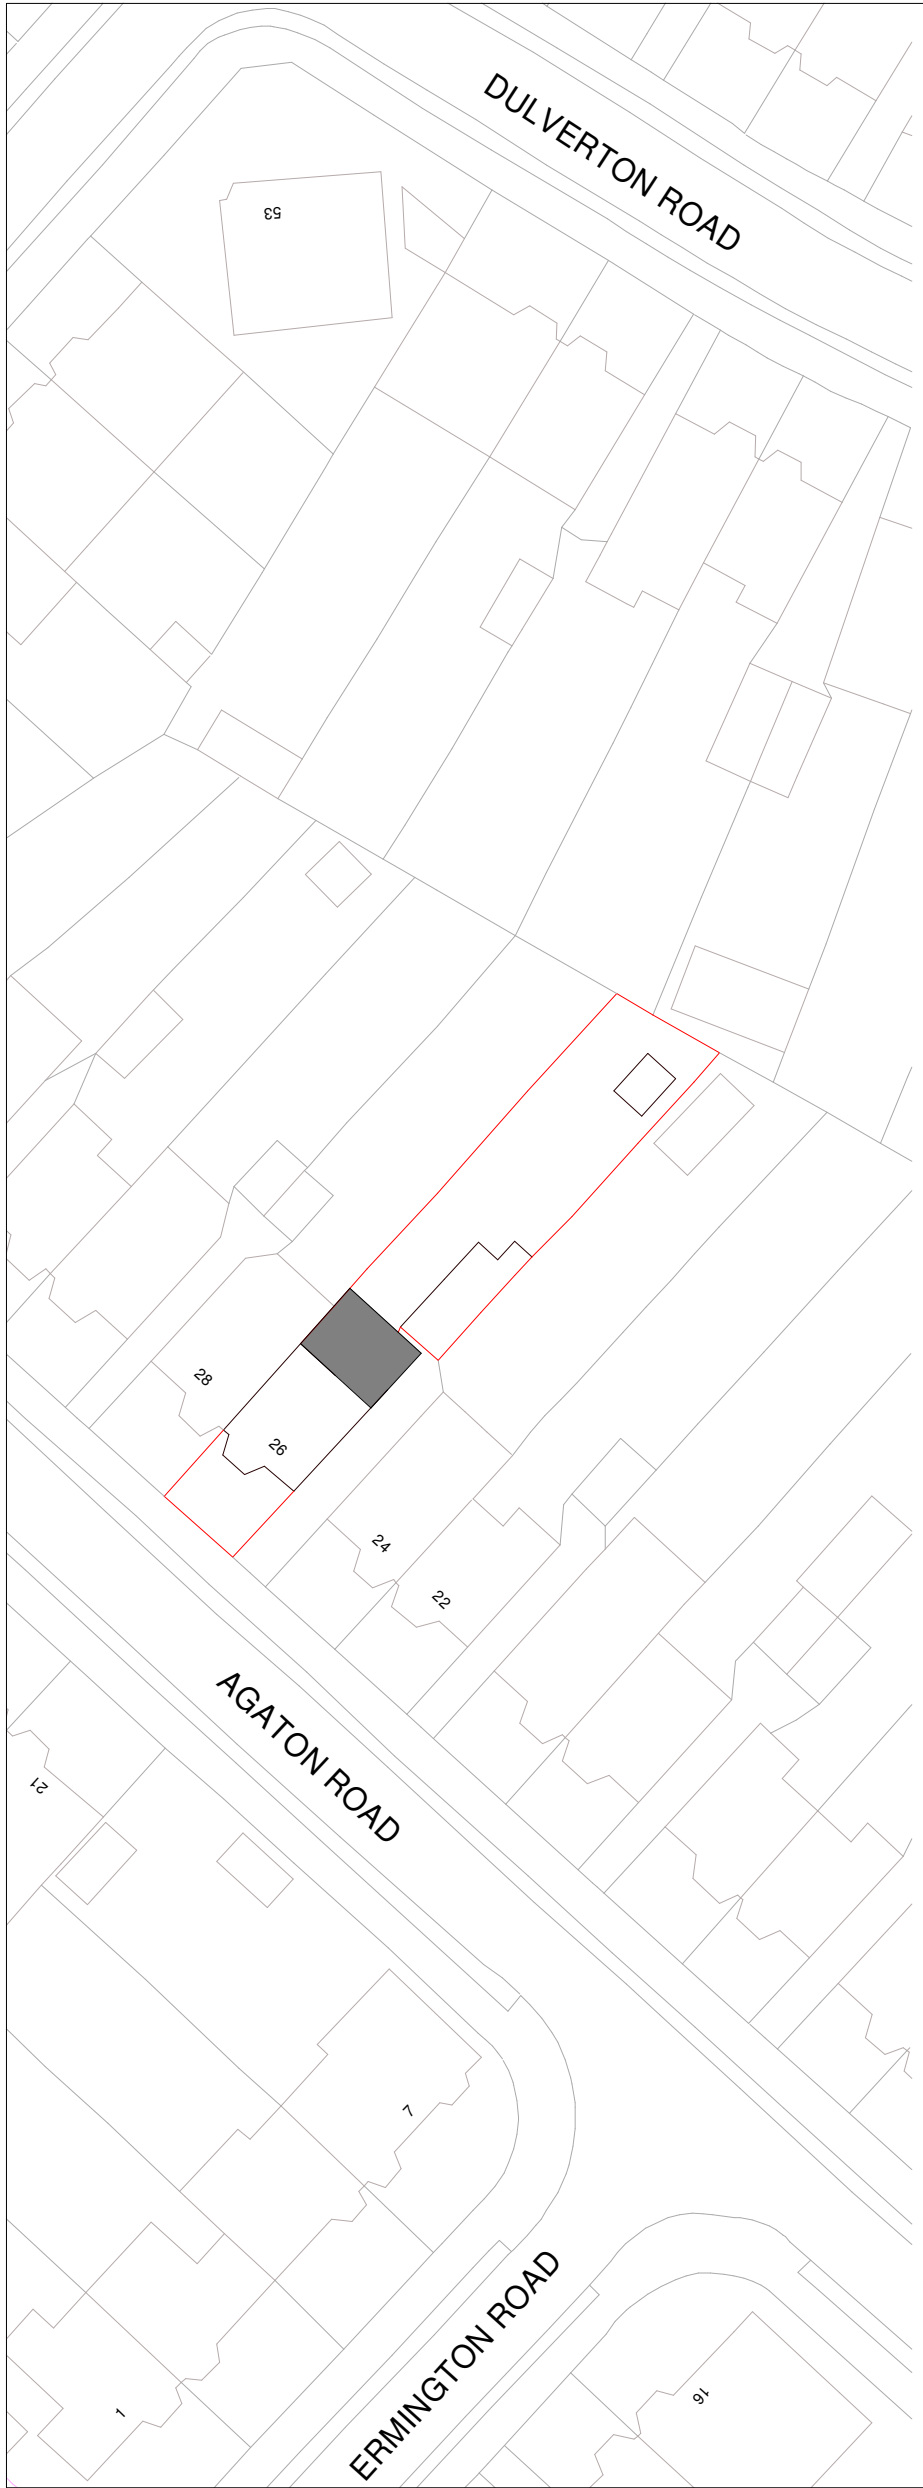

Existing Block Plan
1 : 500

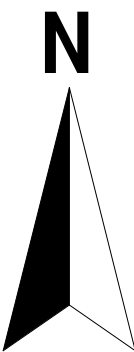

Proposed Block Plan
1 : 500

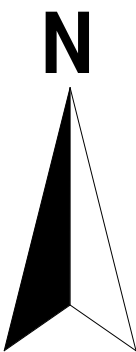

Note to Contractor: Contractor is recommended to carry out an intrusive site investigation prior to commencing works on site to ensure all details designed for this project are appropriate. Contractor to cross reference with Structural Calculations package for suitability, to assess site levels and confirm any design assumptions within the calculations package prior to works commencing on site. If the Contractor requires any additional information, please send a Request For Information to hello@planituk.co.uk before ordering materials and starting the works - requests will be acknowledged and responded to as soon as possible. Please ensure that the drawings have been submitted to Building Control for a Full Plans submission and the compliance report has been discharged before starting works on site. All dimensions must be checked and verified on site by the contractor prior to the commencement of any works. Any discrepancies or variations must be reported to Plan It UK immediately. Do not scale from this drawing. Drain location is an estimated location, contractor to investigate on site and allow a time and cost contingency for adjustments to drainage if required.

Drawn by:
AR

Title Number:

Project:
26 Agaton Road, London, SE9 3RW

Date:
25.06.2026

No:
26-2089


Client:
Emma Chang

Drawing Title:
EXISTING BLOCK PLAN, PROPOSED BLCK
PLAN & LOCATION PLAN



Scale:
1:500,1:1250 @A1,
1:1000,1:2500 @A3

Rev:
00

Page:
D01

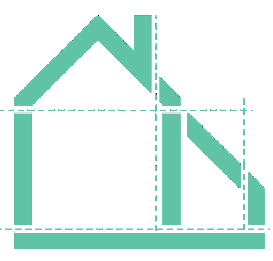
 **Plan It UK**
Architectural Services
7 Leigh House, Bexleyheath, DA7 4QP
Enquiries@planituk.co.uk
Engineer: se@planituk.co.uk

EXISTING

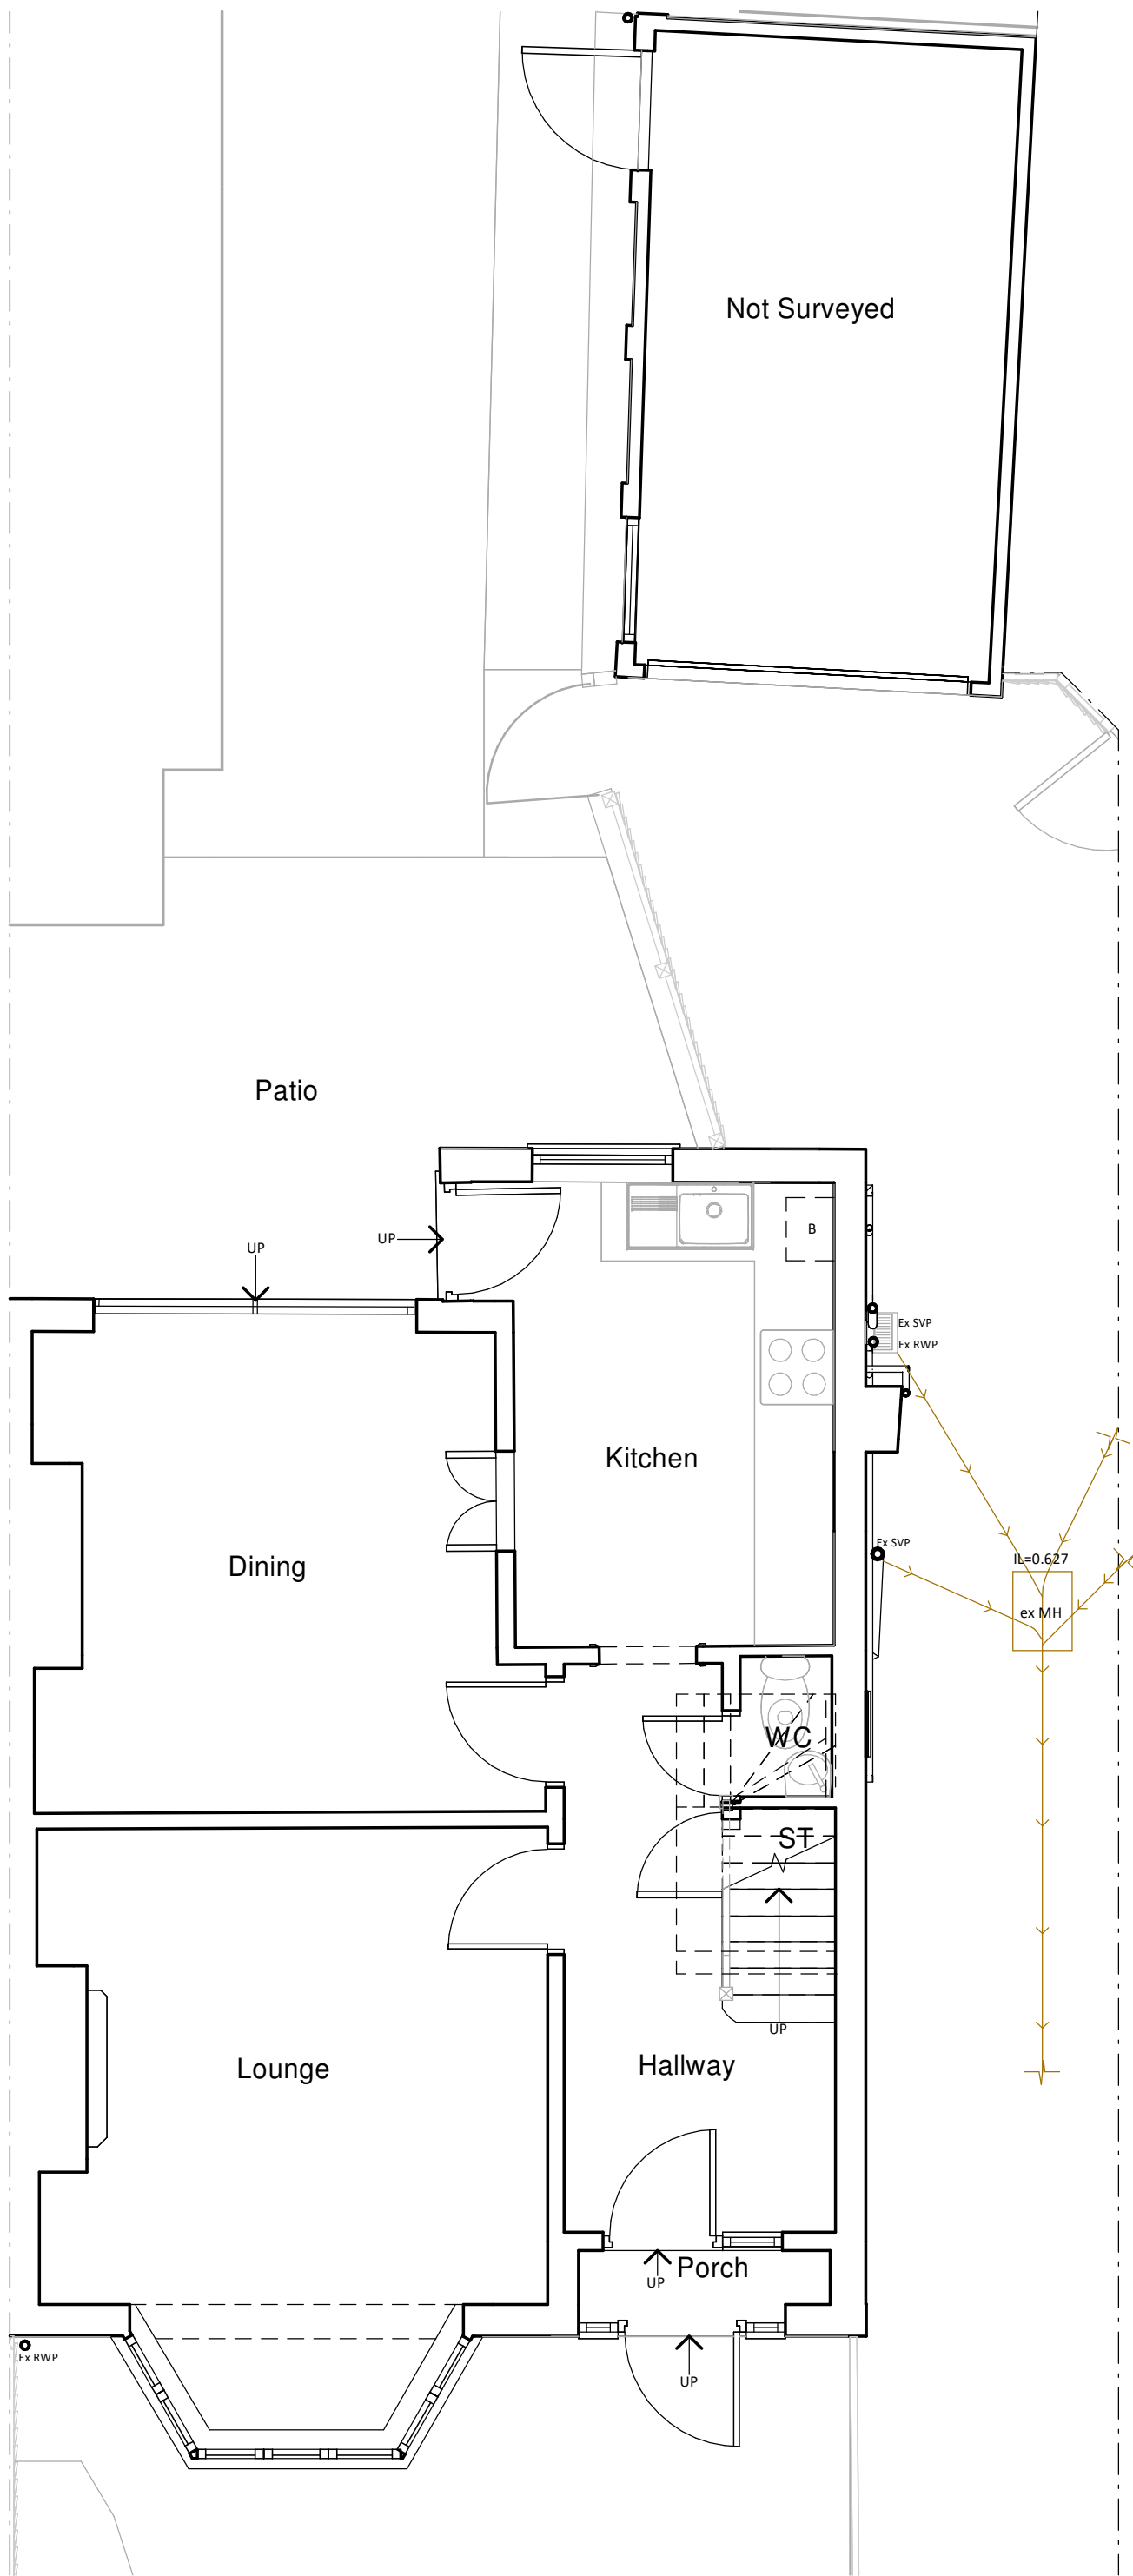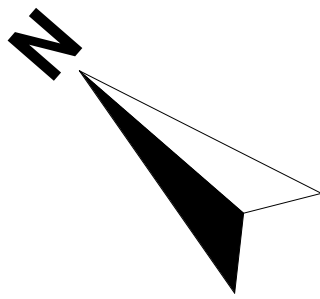

Drainage is assumed – to be investigated
and confirmed prior to works commencing.

Ground Floor Plan
Area ca. 43.20 m²

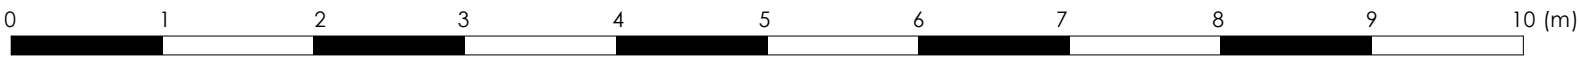


Note to Contractor: Contractor is recommended to carry out an intrusive site investigation prior to commencing works on site to ensure all details designed for this project are appropriate. Contractor to cross reference with Structural Calculations package for suitability, to assess site levels and confirm any design assumptions within the calculations package prior to works commencing on site. If the Contractor requires any additional information, please send a Request For Information to hello@planituk.co.uk before ordering materials and starting the works - requests will be acknowledged and responded to as soon as possible. Please ensure that the drawings have been submitted to Building Control for a Full Plans submission and the compliance report has been discharged before starting works on site. All dimensions must be checked and verified on site by the contractor prior to the commencement of any works. Any discrepancies or variations must be reported to Plan It UK immediately. Do not scale from this drawing. Drain location is an estimated location, contractor to investigate on site and allow a time and cost contingency for adjustments to drainage if required.

Drawn by: AR	Title Number:
Client: Emma Chang	

Project: 26 Agaton Road, London, SE9 3RW	Drawing Title: EXISTING GROUND FLOOR PLAN
---	--



Date: 25.06.2026	Scale: 1:50 @A1, 1:100 @A3
---------------------	-------------------------------

No: 26-2089	Rev: 00	Page: D02
----------------	------------	--------------

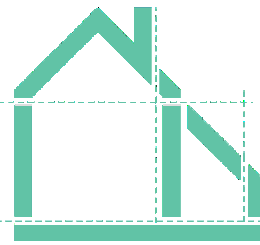

Plan It UK
Architectural Services
7 Leigh House, Bexleyheath, DA7 4QP
Enquiries@planituk.co.uk
Engineer: se@planituk.co.uk

PROPOSED

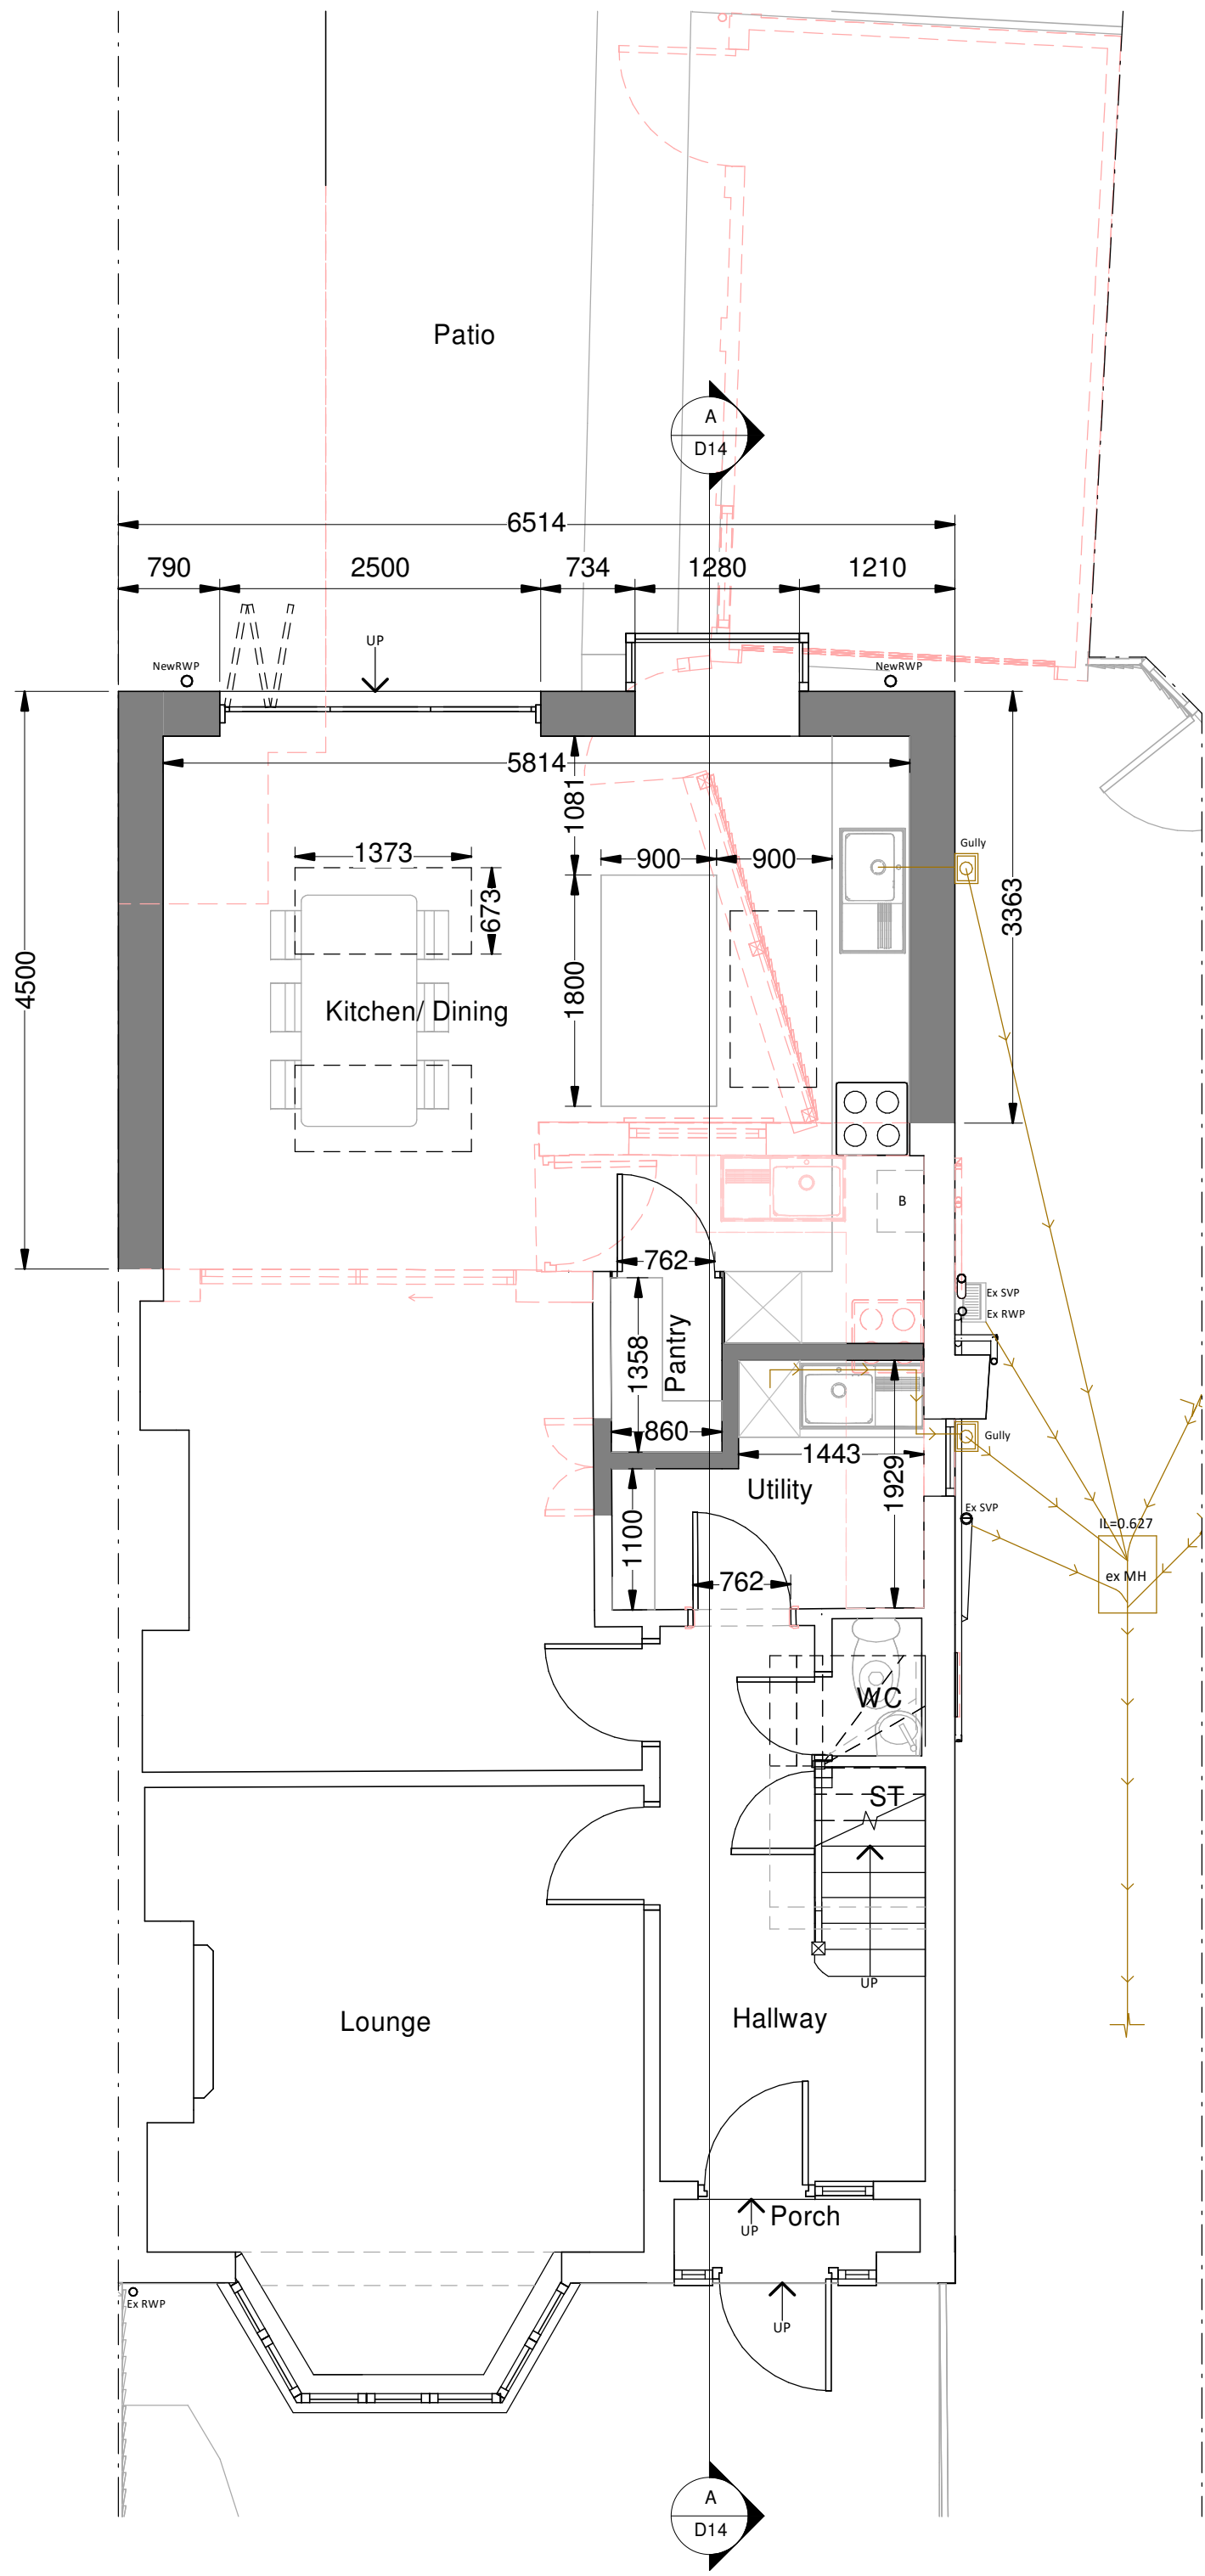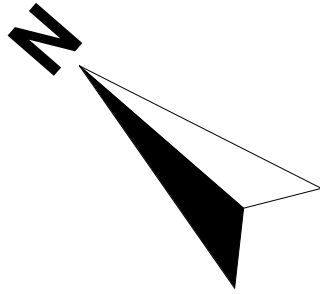

Drainage is assumed – to be investigated and confirmed prior to works commencing.


Symbol Key

- Proposed wall
- Boundary Line
- Details above
- Waste drainage layout
- Demoilshed
- Rainwater layout

Proposed Materials:

- Ground Floor Walls: Render Walls to match existing
- Flat Roof: GRP or single ply membrane
- All new drainage to match materials of existing drainage



Ground Floor Plan
Area ca. 43.20 m²
Additional Area: 22.40 m²

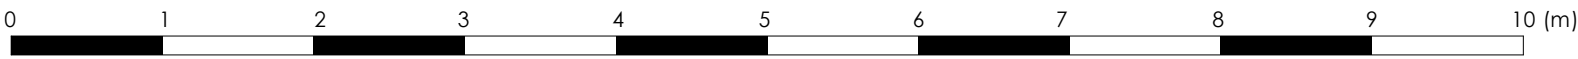


Note to Contractor: Contractor is recommended to carry out an intrusive site investigation prior to commencing works on site to ensure all details designed for this project are appropriate. Contractor to cross reference with Structural Calculations package for suitability, to assess site levels and confirm any design assumptions within the calculations package prior to works commencing on site. If the Contractor requires any additional information, please send a Request For Information to hello@planituk.co.uk before ordering materials and starting the works - requests will be acknowledged and responded to as soon as possible. Please ensure that the drawings have been submitted to Building Control for a Full Plans submission and the compliance report has been discharged before starting works on site. All dimensions must be checked and verified on site by the contractor prior to the commencement of any works. Any discrepancies or variations must be reported to Plan It UK immediately. Do not scale from this drawing. Drain location is an estimated location, contractor to investigate on site and allow a time and cost contingency for adjustments to drainage if required.

Drawn by: AR	Title Number:	Project: 26 Agaton Road, London, SE9 3RW	Date: 25.06.2026	No: 26-2089	 7 Leigh House, Bexleyheath, DA7 4QP Enquiries@planituk.co.uk Engineer: se@planituk.co.uk
Client: Emma Chang		Drawing Title: PROPOSED GROUND FLOOR PLAN	Scale: 1:50 @A1, 1:100 @A3	Rev: 00	
				Page: D03	

EXISTING

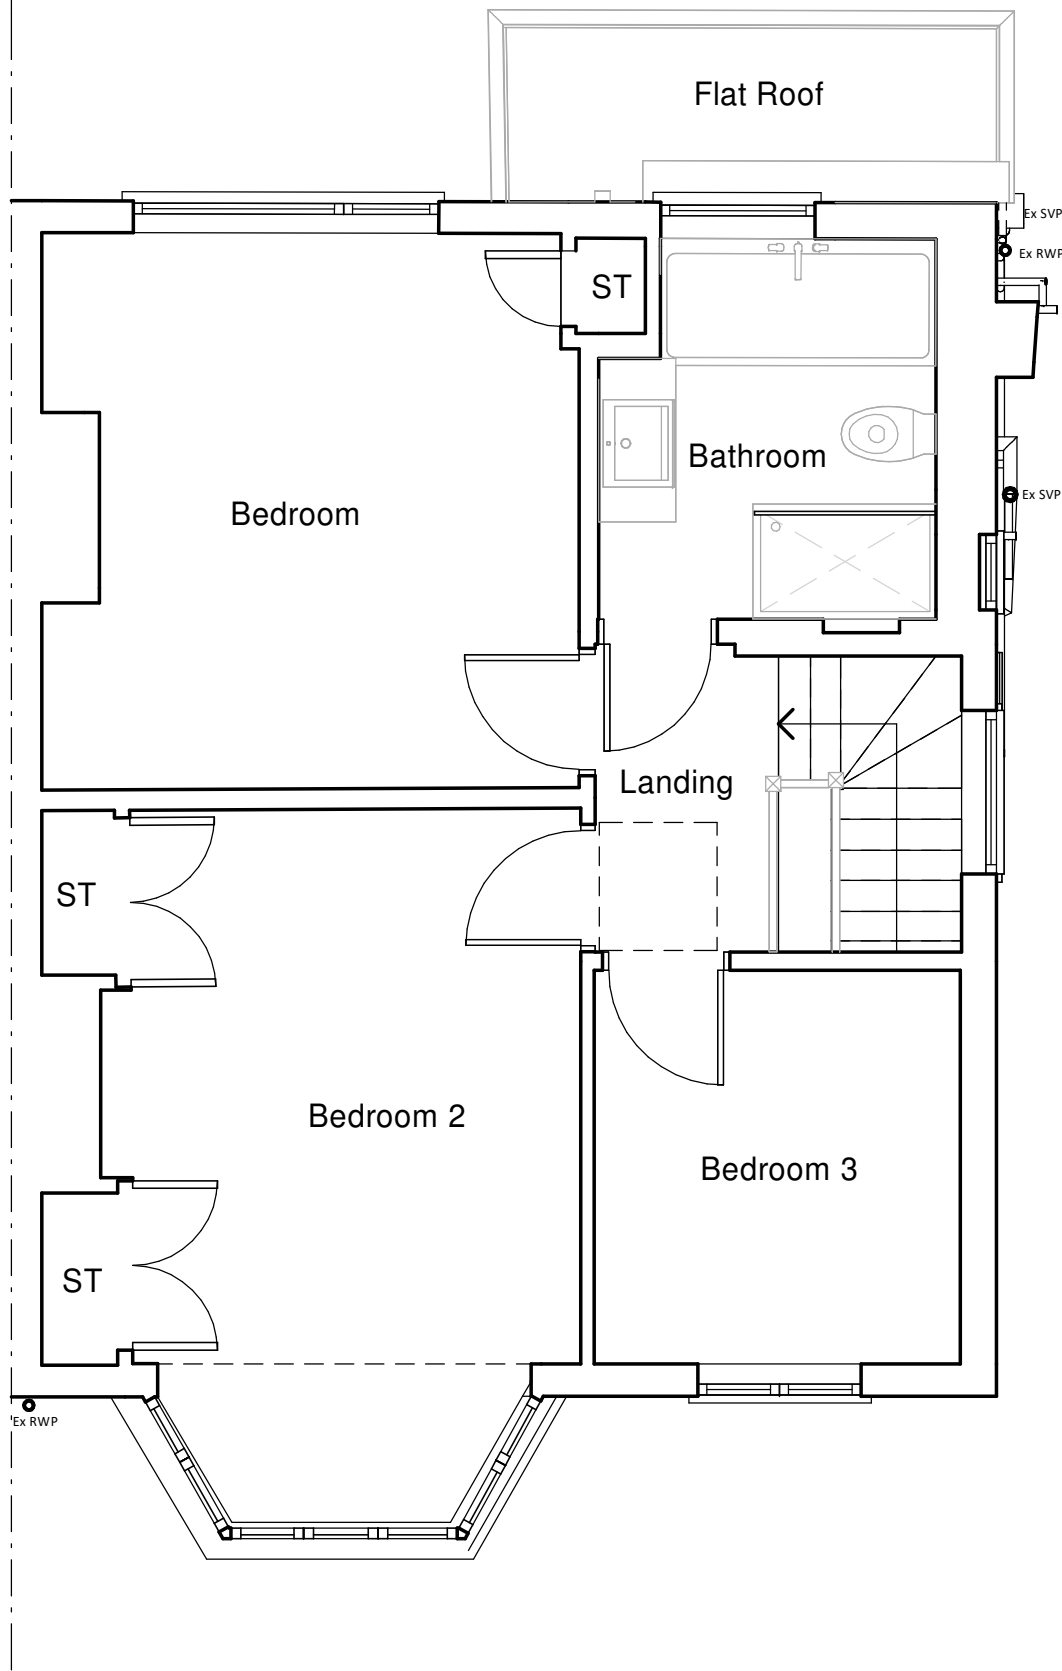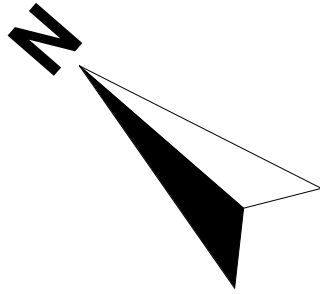

First Floor Plan
Area ca. 40.68 m²

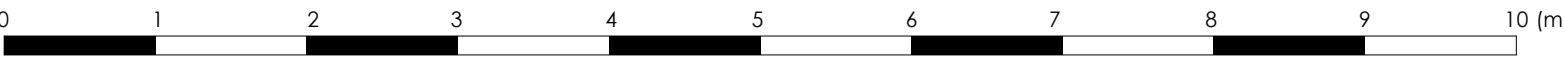


Note to Contractor: Contractor is recommended to carry out an intrusive site investigation prior to commencing works on site to ensure all details designed for this project are appropriate. Contractor to cross reference with Structural Calculations package for suitability, to assess site levels and confirm any design assumptions within the calculations package prior to works commencing on site. If the Contractor requires any additional information, please send a Request For Information to hello@planituk.co.uk before ordering materials and starting the works - requests will be acknowledged and responded to as soon as possible. Please ensure that the drawings have been submitted to Building Control for a Full Plans submission and the compliance report has been discharged before starting works on site. All dimensions must be checked and verified on site by the contractor prior to the commencement of any works. Any discrepancies or variations must be reported to Plan It UK immediately. Do not scale from this drawing. Drain location is an estimated location, contractor to investigate on site and allow a time and cost contingency for adjustments to drainage if required.

Drawn by: AR	Title Number:
Client: Emma Chang	

Project: 26 Agaton Road, London, SE9 3RW	Drawing Title: EXISTING FIRST FLOOR PLAN
---	---



Date: 25.06.2026	Scale: 1:50 @A1, 1:100 @A3
---------------------	-------------------------------

No: 26-2089
Rev: 00
Page: D04

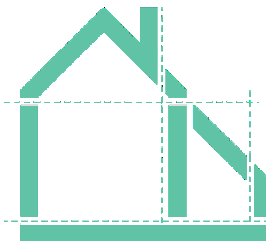

Plan It UK
Architectural Services
7 Leigh House, Bexleyheath, DA7 4QP
Enquiries@planituk.co.uk
Engineer: se@planituk.co.uk

PROPOSED

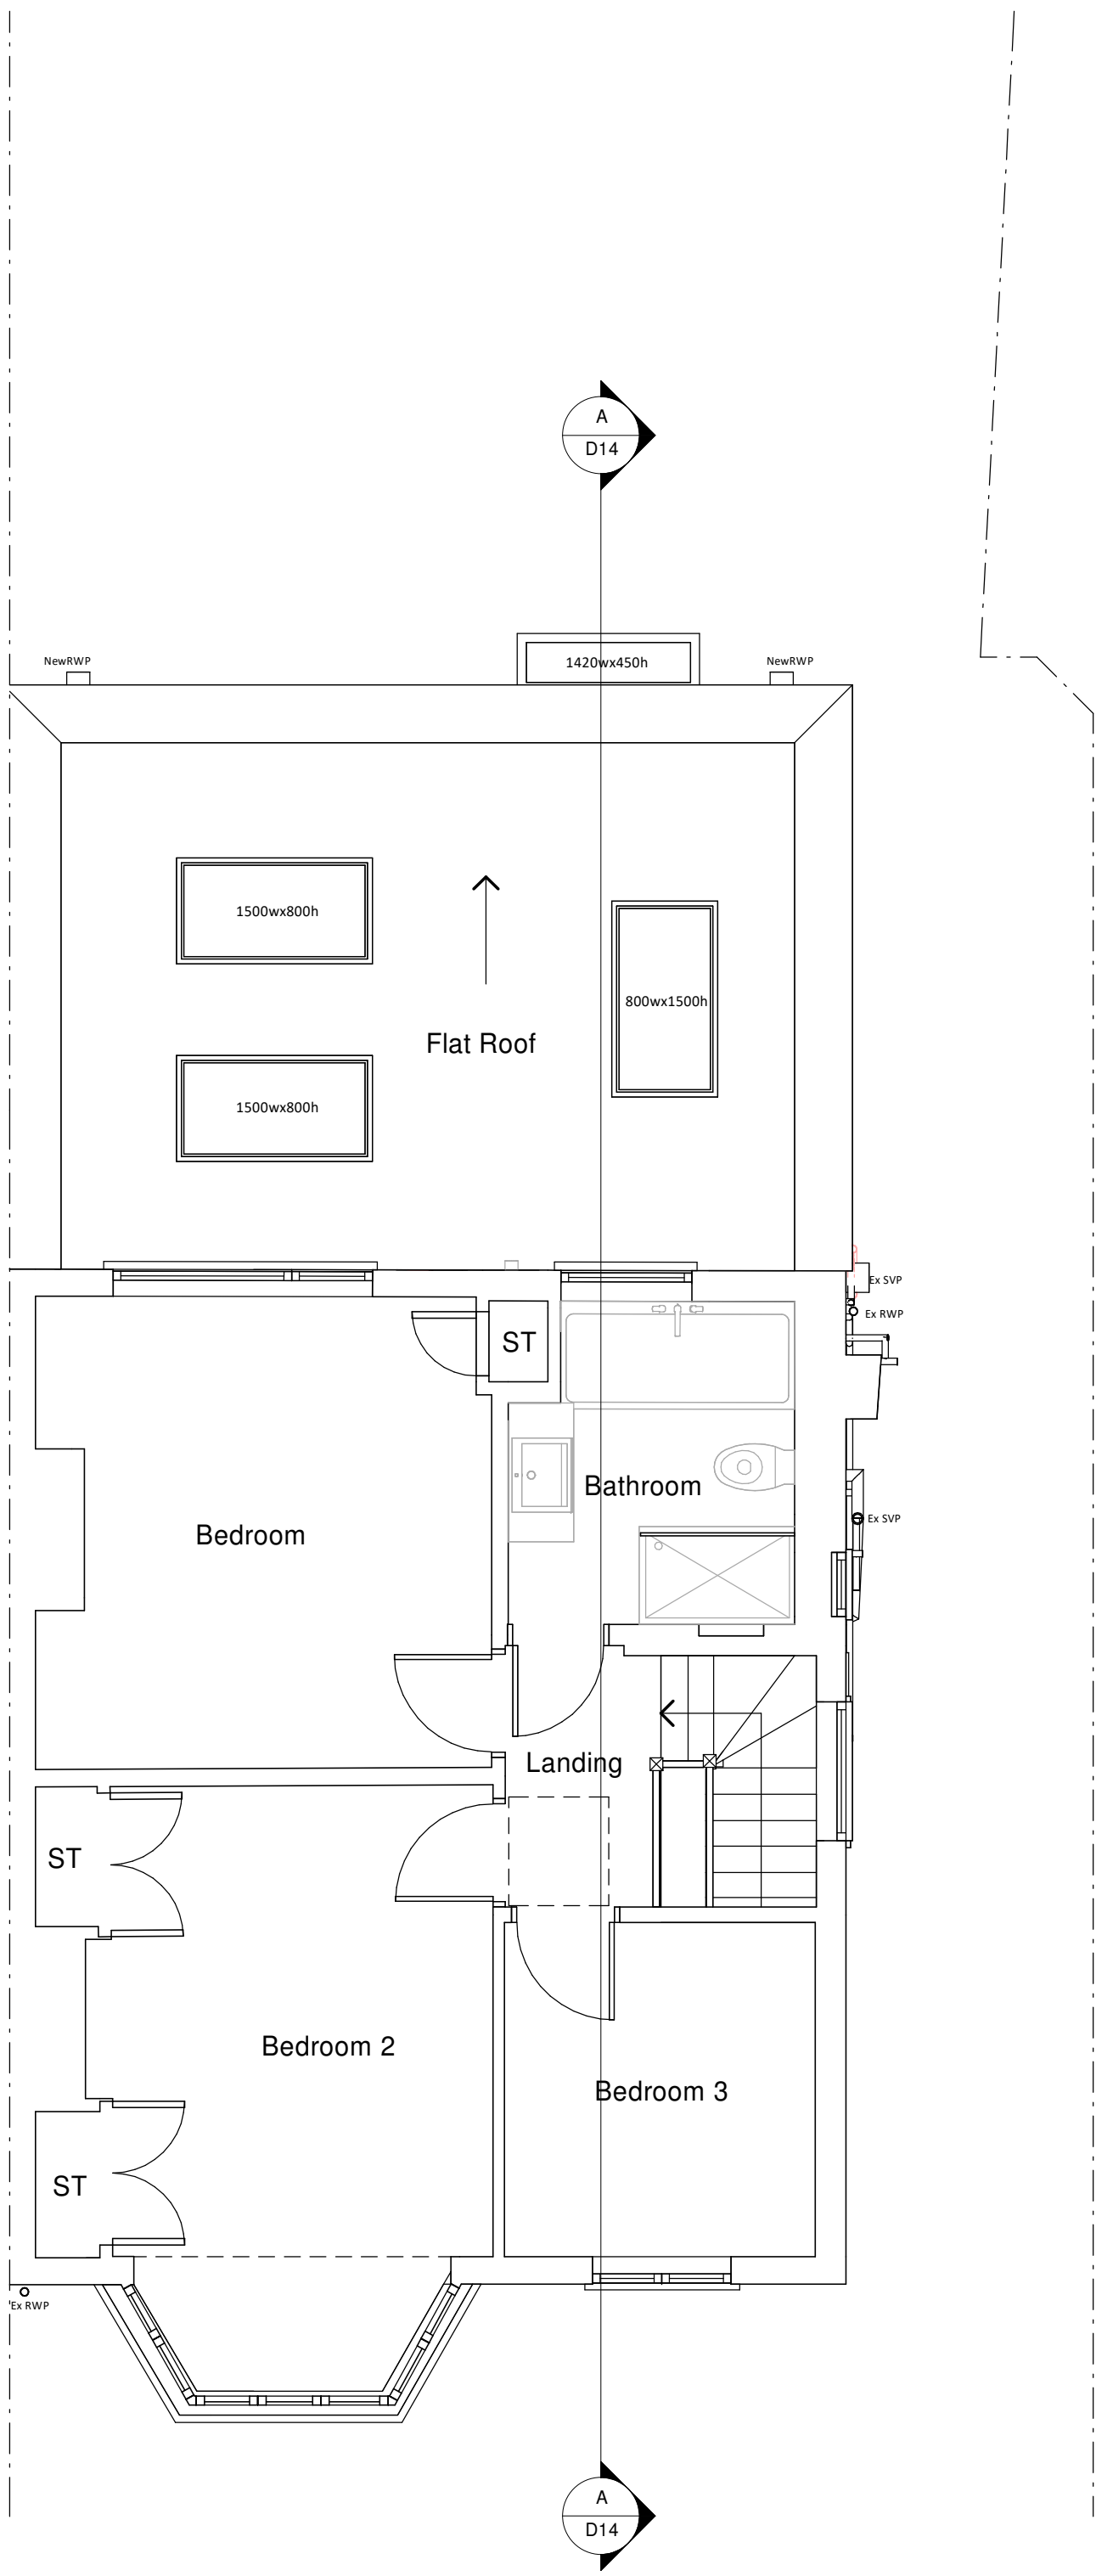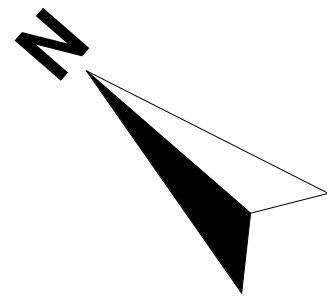


First Floor Plan

Area ca. 40.68 m²

- Symbol Key
- Proposed wall
 - Boundary Line
 - Details above
 - Waste drainage layout
 - Demoilshed
 - Rainwater layout

Proposed Materials:
Ground Floor Walls: Render Walls to match existing
Flat Roof: GRP or single ply membrane
All new drainage to match materials of existing drainage

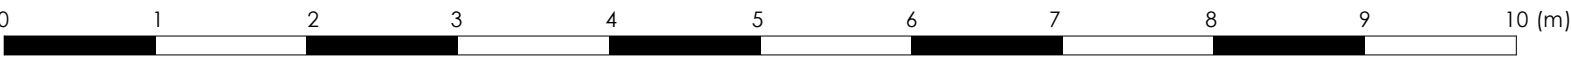

Note to Contractor: Contractor is recommended to carry out an intrusive site investigation prior to commencing works on site to ensure all details designed for this project are appropriate. Contractor to cross reference with Structural Calculations package for suitability, to assess site levels and confirm any design assumptions within the calculations package prior to works commencing on site. If the Contractor requires any additional information, please send a Request For Information to hello@planituk.co.uk before ordering materials and starting the works - requests will be acknowledged and responded to as soon as possible. Please ensure that the drawings have been submitted to Building Control for a Full Plans submission and the compliance report has been discharged before starting works on site. All dimensions must be checked and verified on site by the contractor prior to the commencement of any works. Any discrepancies or variations must be reported to Plan It UK immediately. Do not scale from this drawing. Drain location is an estimated location, contractor to investigate on site and allow a time and cost contingency for adjustments to drainage if required.

Drawn by:
AR

Title Number:

Project:
26 Agaton Road, London, SE9 3RW

Date:
25.06.2026

No:
26-2089

Rev:
00

Page:
D05

Client:
Emma Chang



Drawing Title:
PROPOSED FIRST FLOOR PLAN

Scale:
1:50 @A1, 1:100 @A3



7 Leigh House, Bexleyheath, DA7 4QP
Enquiries@planituk.co.uk
Engineer: se@planituk.co.uk

EXISTING

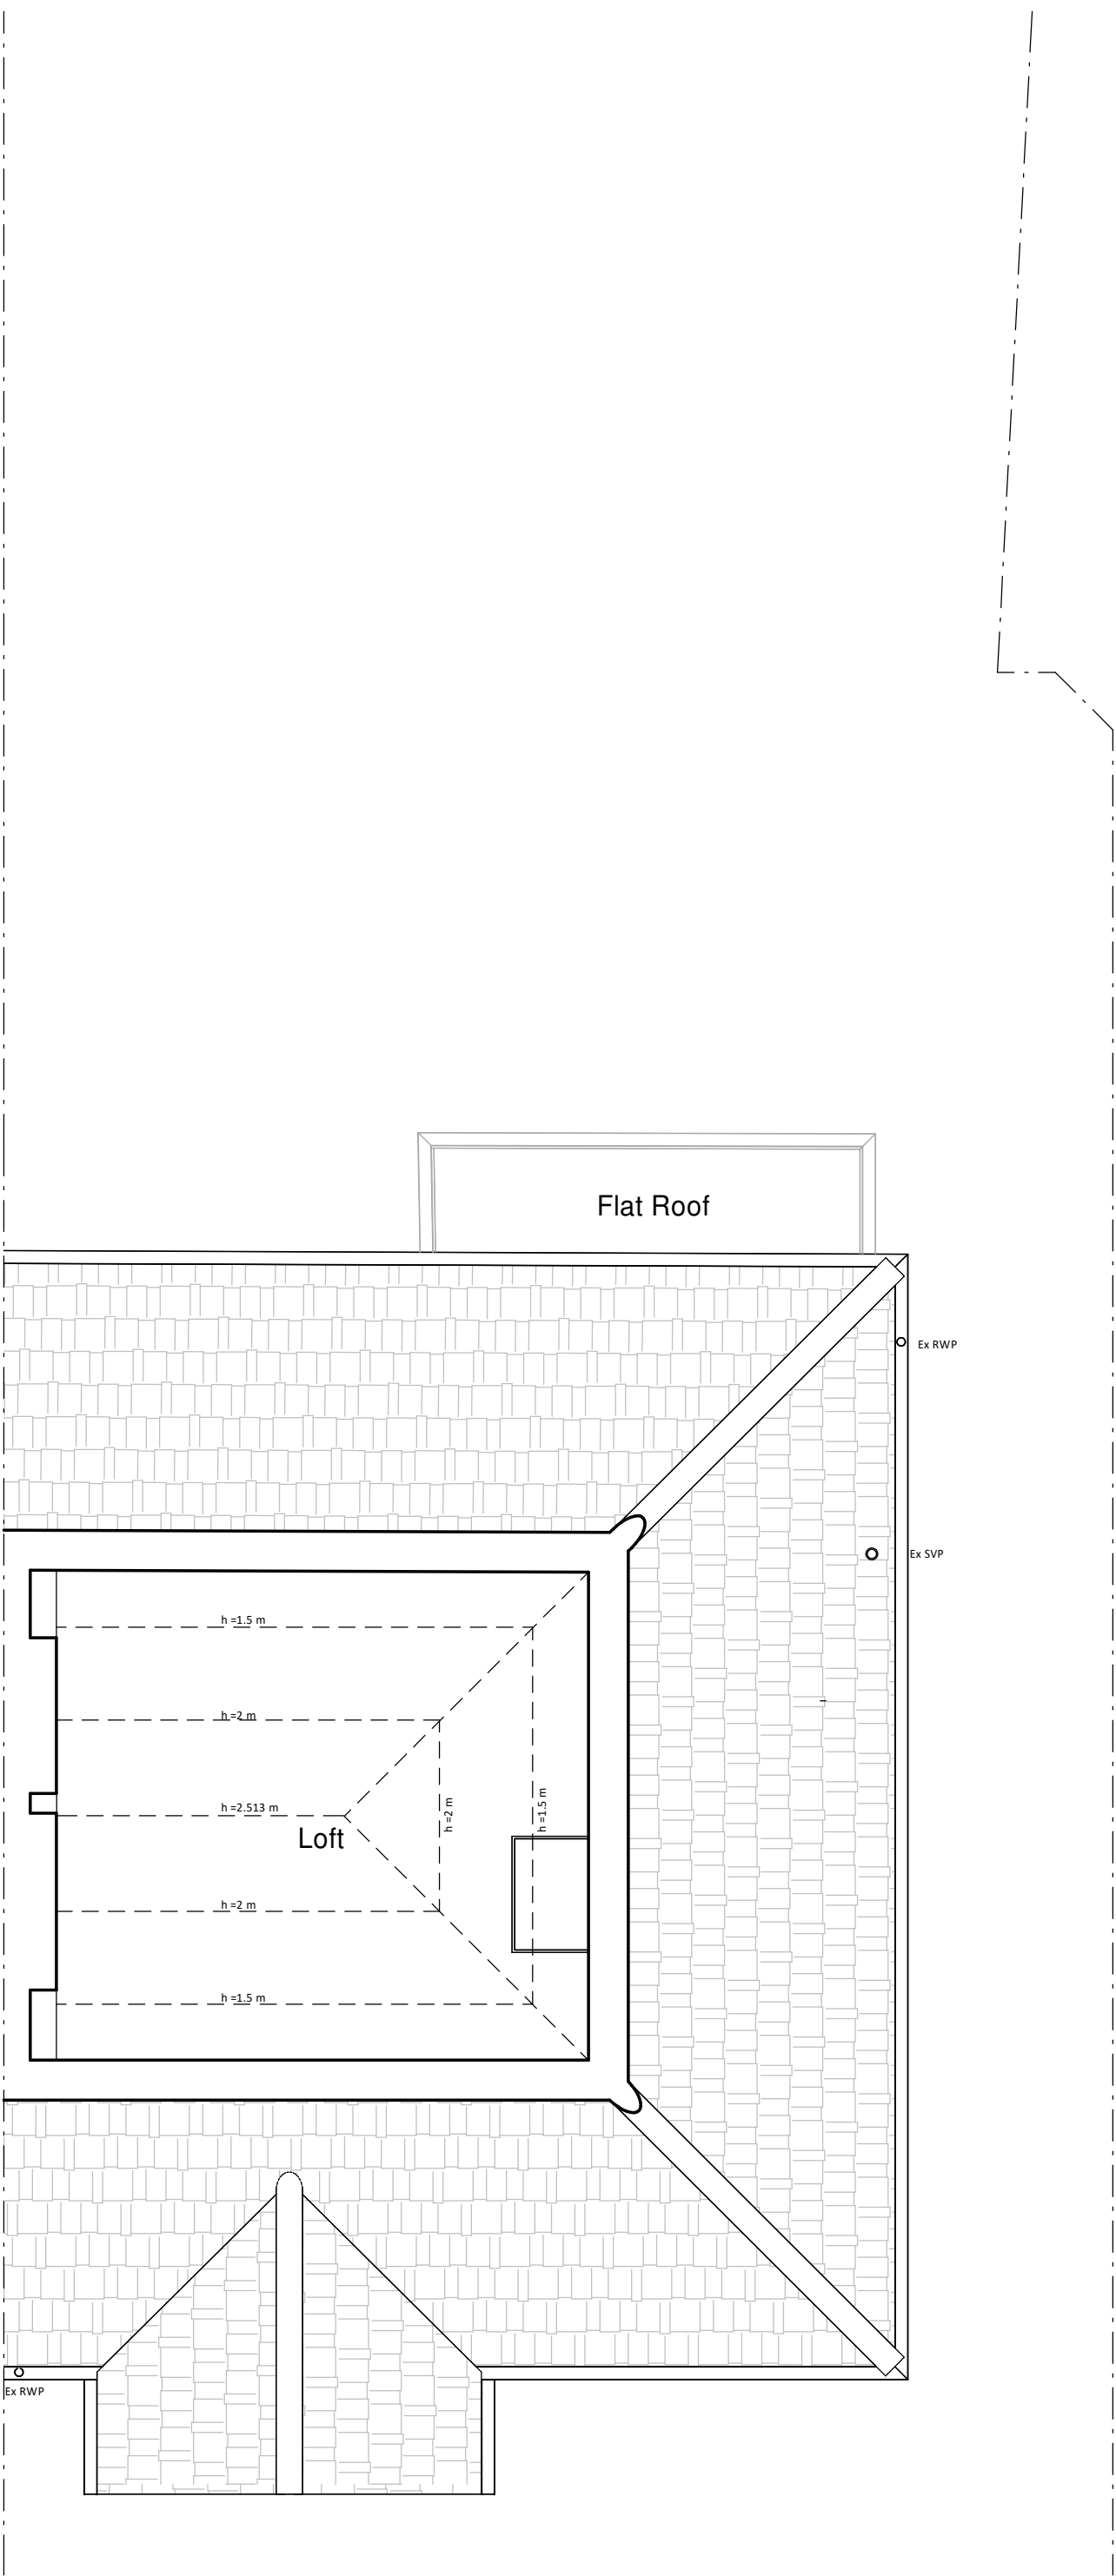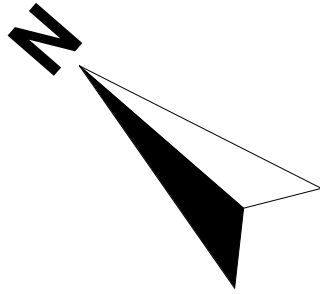

Loft Plan

Area ca. 43.93 m²

Note to Contractor: Contractor is recommended to carry out an intrusive site investigation prior to commencing works on site to ensure all details designed for this project are appropriate. Contractor to cross reference with Structural Calculations package for suitability, to assess site levels and confirm any design assumptions within the calculations package prior to works commencing on site. If the Contractor requires any additional information, please send a Request For Information to hello@planituk.co.uk before ordering materials and starting the works - requests will be acknowledged and responded to as soon as possible. Please ensure that the drawings have been submitted to Building Control for a Full Plans submission and the compliance report has been discharged before starting works on site. All dimensions must be checked and verified on site by the contractor prior to the commencement of any works. Any discrepancies or variations must be reported to Plan It UK immediately. Do not scale from this drawing. Drain location is an estimated location, contractor to investigate on site and allow a time and cost contingency for adjustments to drainage if required.

Drawn by:
AR

Title Number:

Project:
26 Agaton Road, London, SE9 3RW

Date:
25.06.2026

No:
26-2089

Rev:
00

Page:
D06



7 Leigh House, Bexleyheath, DA7 4QP

Enquiries@planituk.co.uk



Engineer: se@planituk.co.uk

Client:
Emma Chang

Drawing Title:
EXISTING LOFT PLAN

Scale:
1:50 @A1, 1:100 @A3

PROPOSED

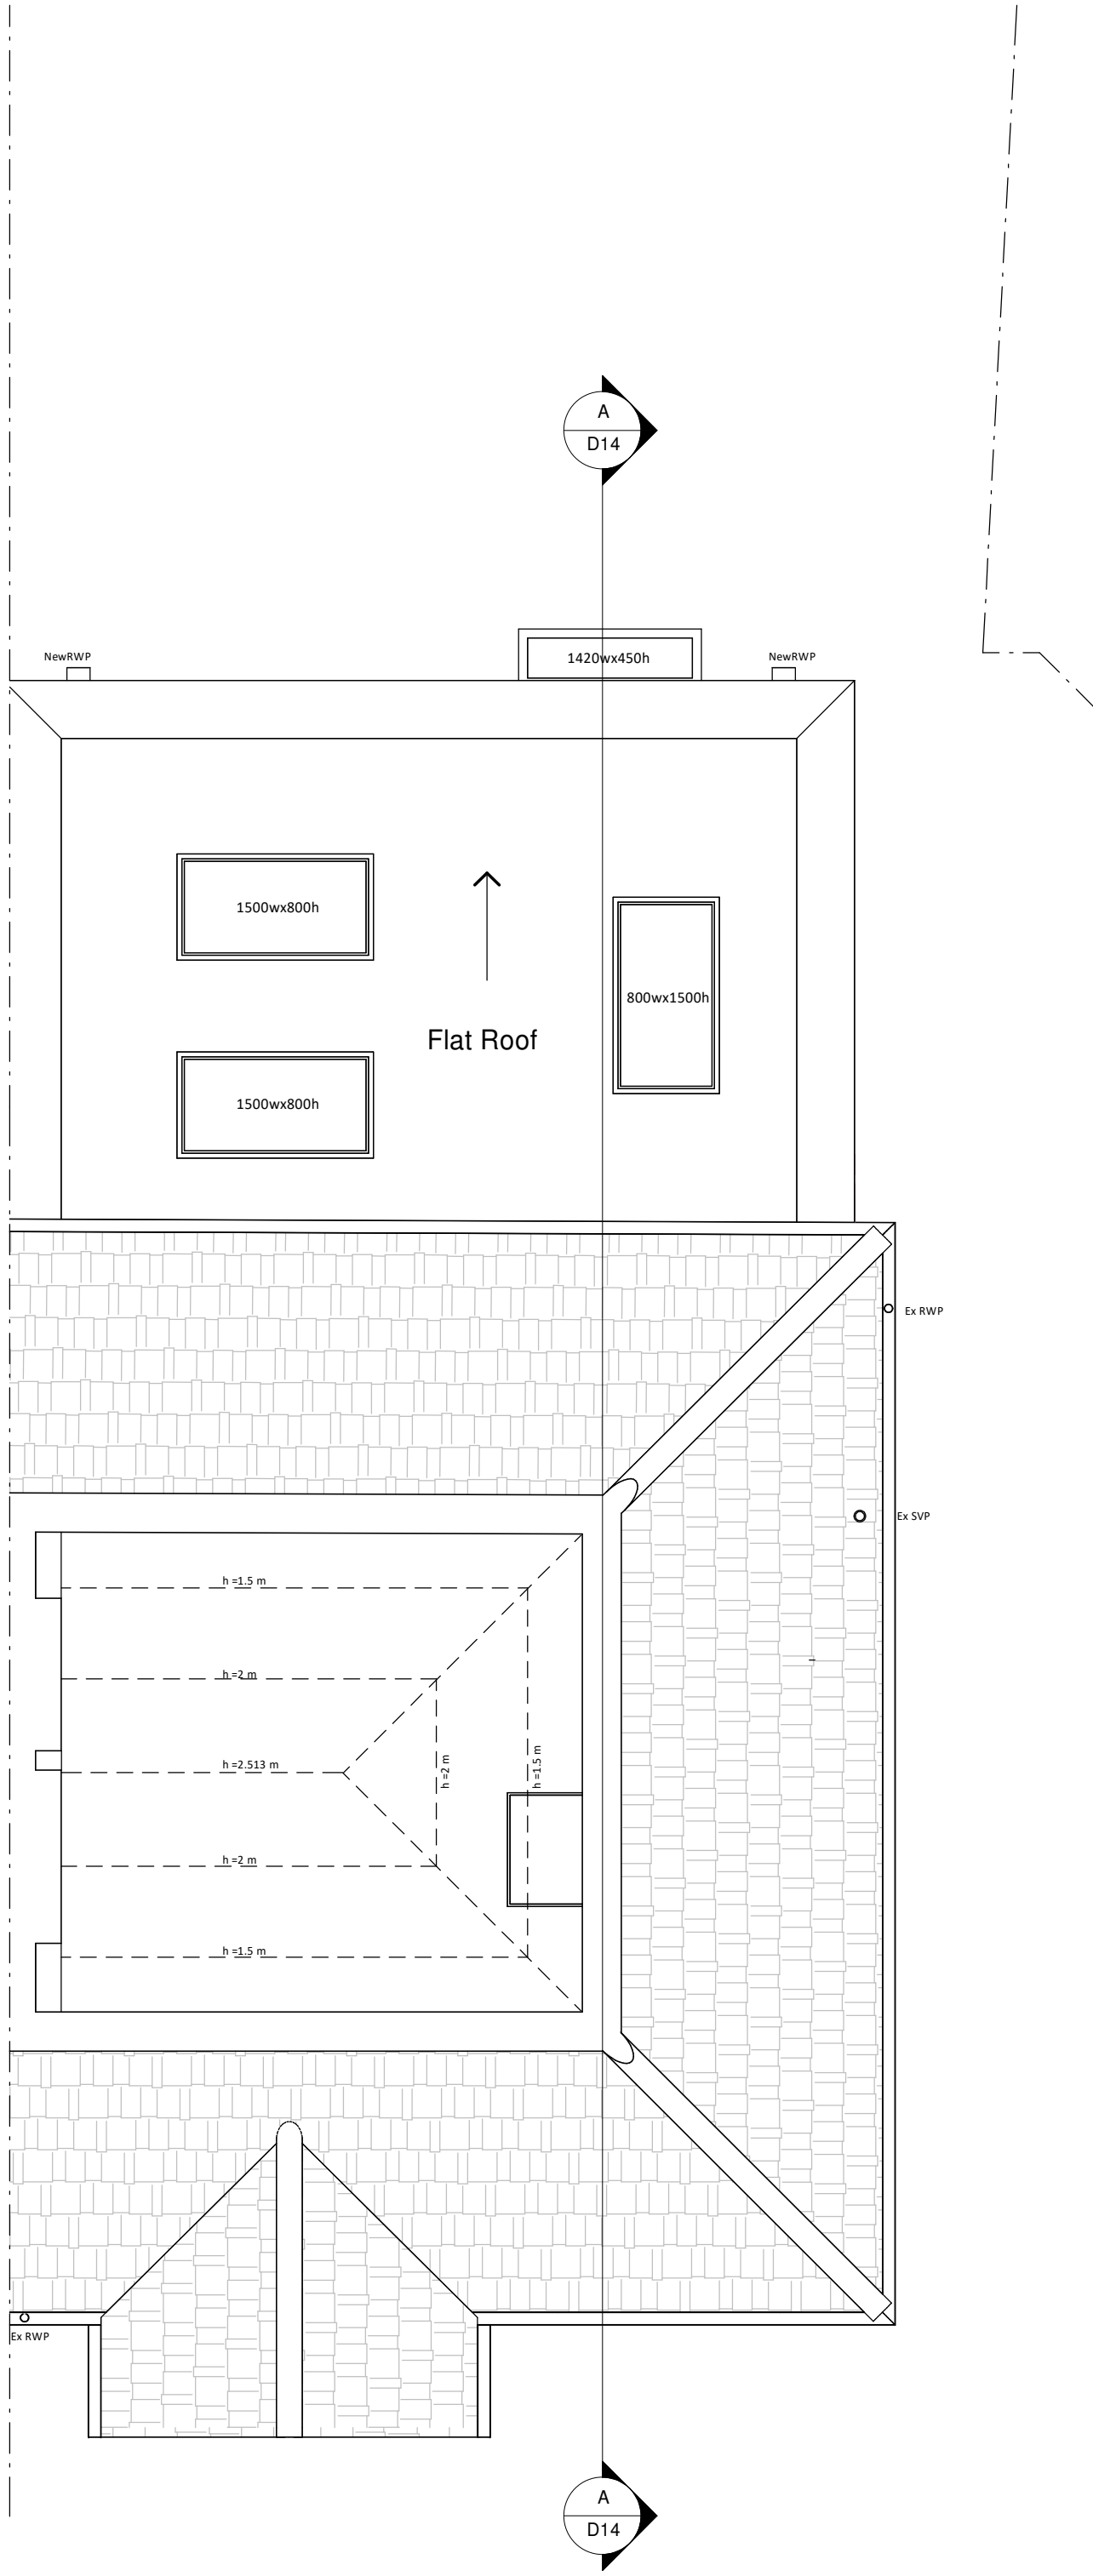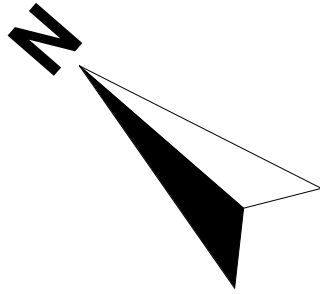


Loft Plan

Area ca. 43.93 m²

- Symbol Key
- Proposed wall
 - Boundary Line
 - Details above
 - Waste drainage layout
 - Demoilshed
 - Rainwater layout

Proposed Materials:
Ground Floor Walls: Render Walls to match existing
Flat Roof: GRP or single ply membrane
All new drainage to match materials of existing drainage

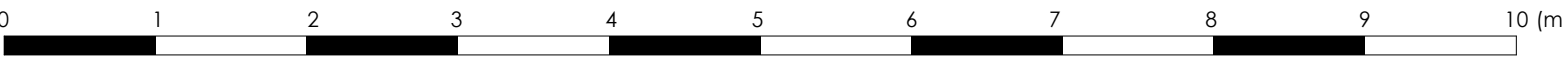

Note to Contractor: Contractor is recommended to carry out an intrusive site investigation prior to commencing works on site to ensure all details designed for this project are appropriate. Contractor to cross reference with Structural Calculations package for suitability, to assess site levels and confirm any design assumptions within the calculations package prior to works commencing on site. If the Contractor requires any additional information, please send a Request For Information to hello@planituk.co.uk before ordering materials and starting the works - requests will be acknowledged and responded to as soon as possible. Please ensure that the drawings have been submitted to Building Control for a Full Plans submission and the compliance report has been discharged before starting works on site. All dimensions must be checked and verified on site by the contractor prior to the commencement of any works. Any discrepancies or variations must be reported to Plan It UK immediately. Do not scale from this drawing. Drain location is an estimated location, contractor to investigate on site and allow a time and cost contingency for adjustments to drainage if required.

Drawn by:
AR

Title Number:

Project:
26 Agaton Road, London, SE9 3RW

Date:
25.06.2026

No:
26-2089


Rev:
00

Page:
D07

Client:
Emma Chang

Drawing Title:
PROPOSED LOFT PLAN

Scale:
1:50 @A1, 1:100 @A3

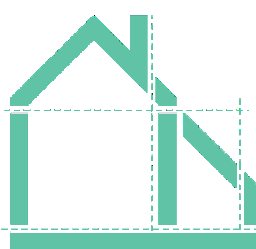

Plan It UK



Architectural Services

7 Leigh House, Bexleyheath, DA7 4QP


Enquiries@planituk.co.uk

Engineer: se@planituk.co.uk

EXISTING

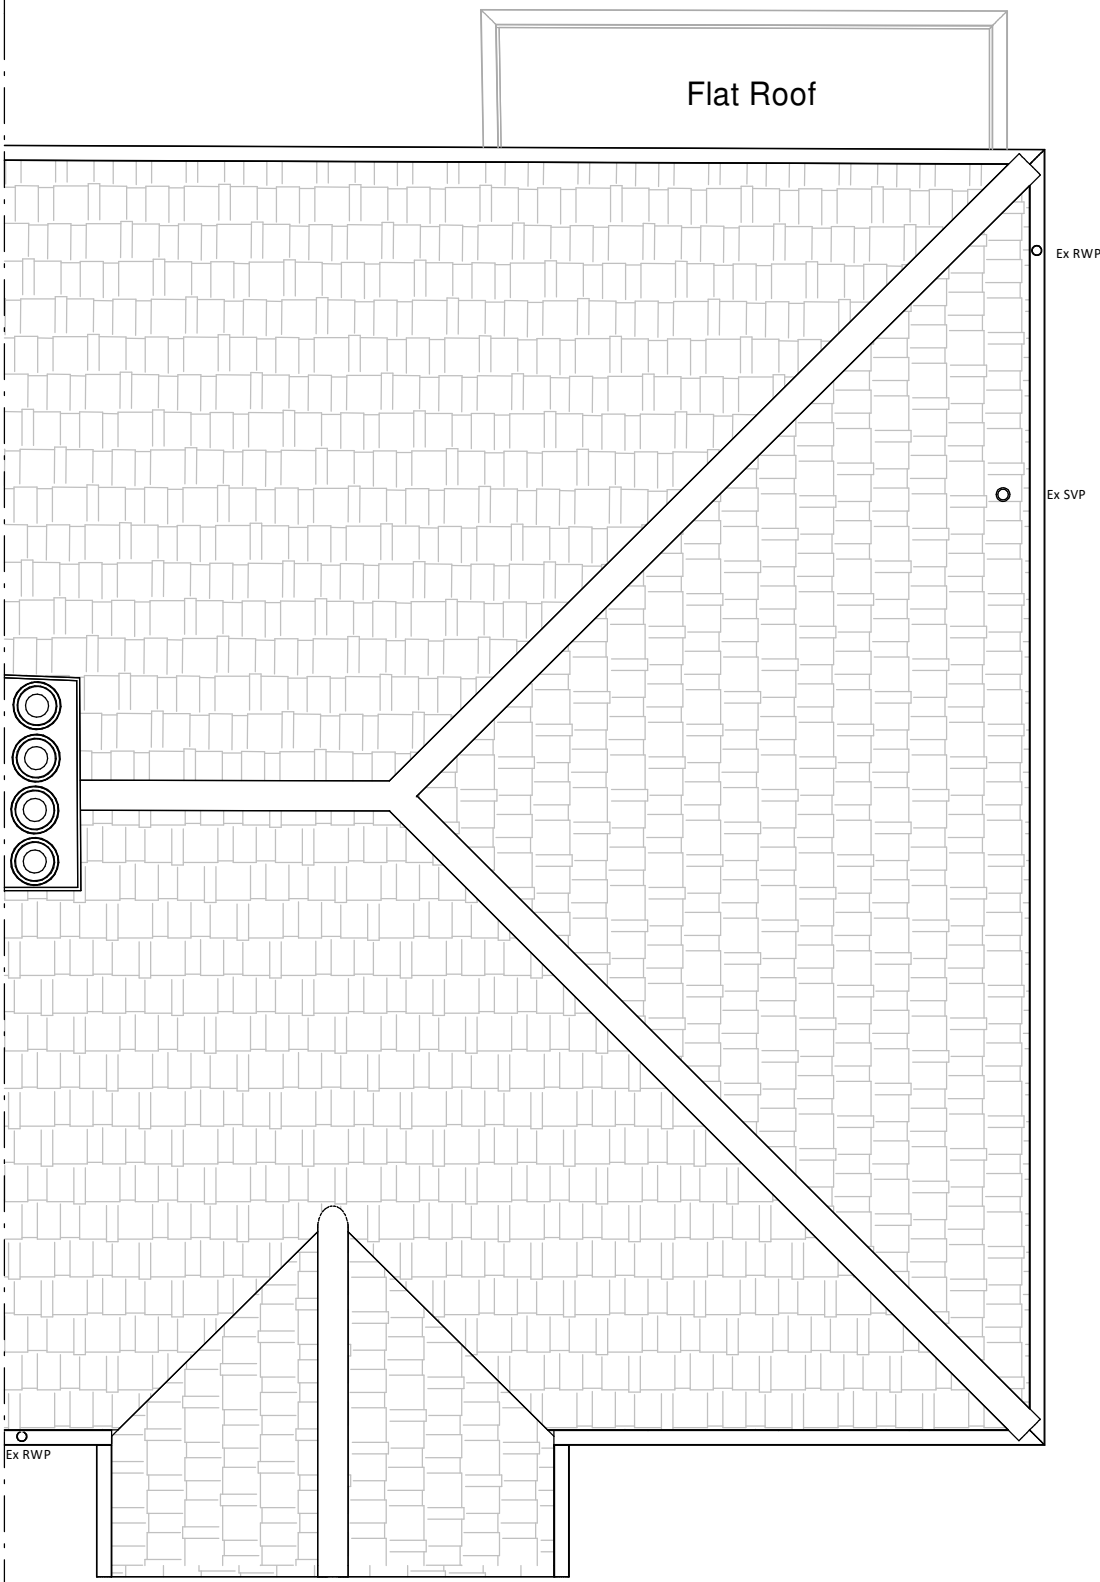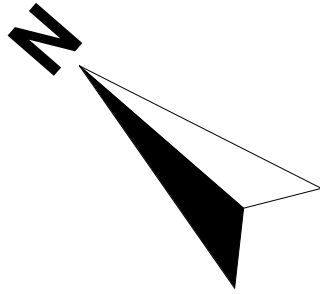

Roof Plan

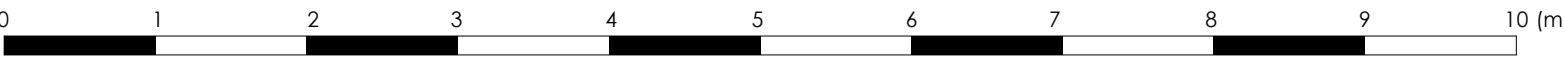

Note to Contractor: Contractor is recommended to carry out an intrusive site investigation prior to commencing works on site to ensure all details designed for this project are appropriate. Contractor to cross reference with Structural Calculations package for suitability, to assess site levels and confirm any design assumptions within the calculations package prior to works commencing on site. If the Contractor requires any additional information, please send a Request For Information to hello@planituk.co.uk before ordering materials and starting the works - requests will be acknowledged and responded to as soon as possible. Please ensure that the drawings have been submitted to Building Control for a Full Plans submission and the compliance report has been discharged before starting works on site. All dimensions must be checked and verified on site by the contractor prior to the commencement of any works. Any discrepancies or variations must be reported to Plan It UK immediately. Do not scale from this drawing. Drain location is an estimated location, contractor to investigate on site and allow a time and cost contingency for adjustments to drainage if required.

Drawn by:
AR

Title Number:

Project:
26 Agaton Road, London, SE9 3RW

Date:
25.06.2026

No:
26-2089


Rev:
00

Page:
D08

Client:
Emma Chang



Drawing Title:
EXISTING ROOF PLAN

Scale:
1:50 @A1, 1:100 @A3

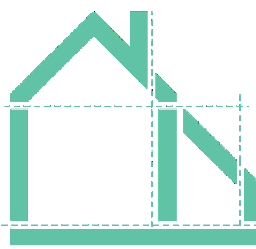

Plan It UK
Architectural Services
7 Leigh House, Bexleyheath, DA7 4QP
Enquiries@planituk.co.uk
Engineer: se@planituk.co.uk


PROPOSED

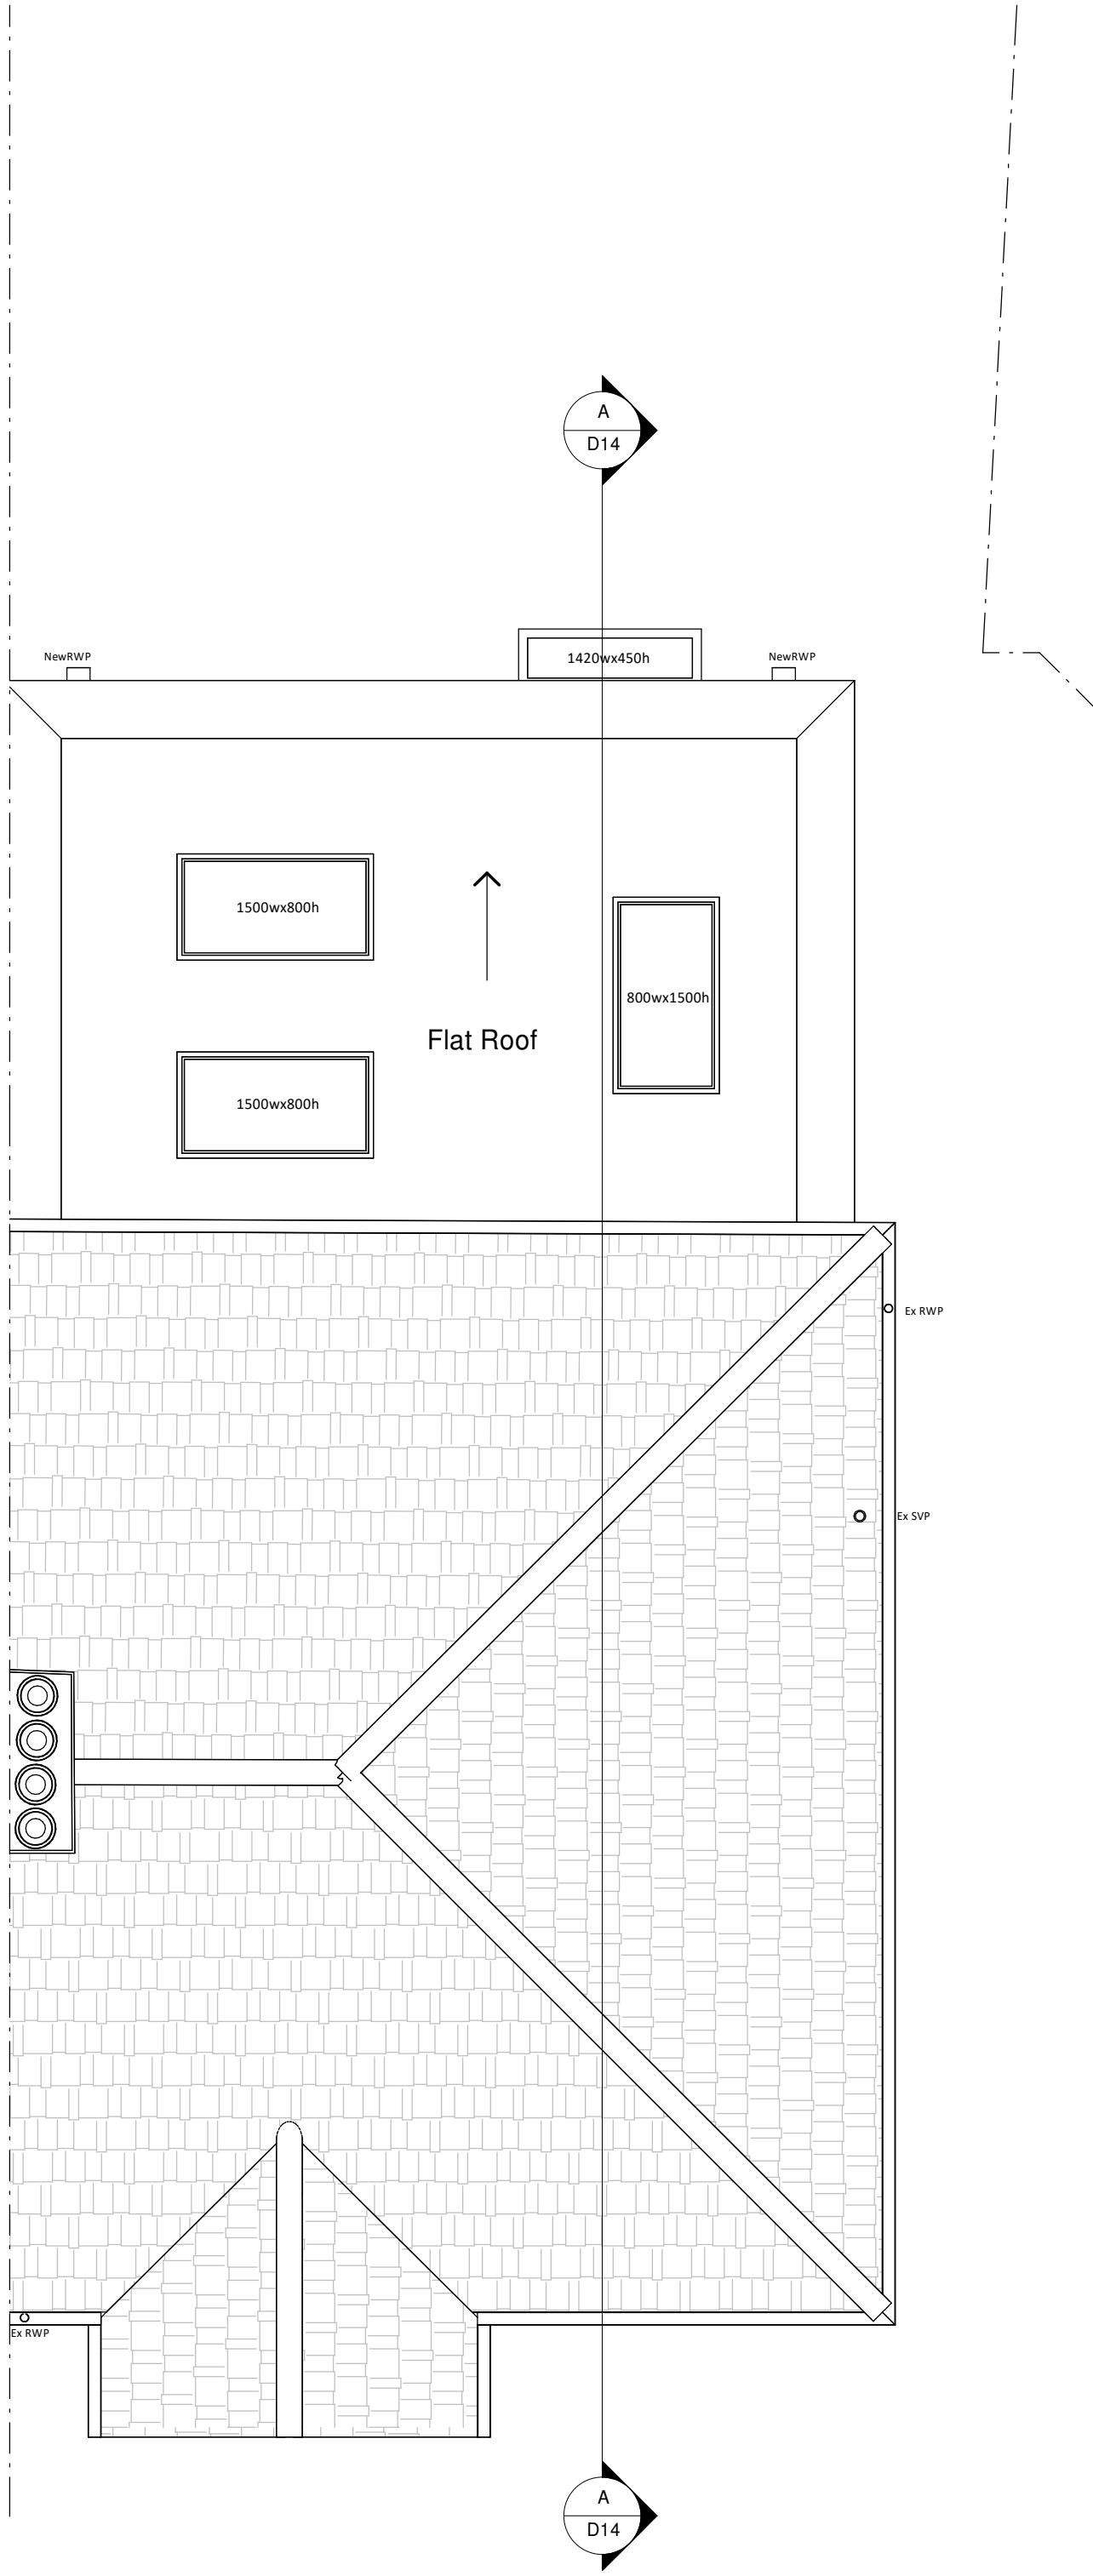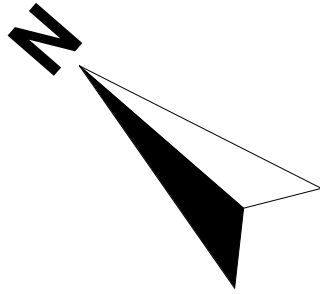

Roof Plan

- Symbol Key
- Proposed wall
 - Boundary Line
 - Details above
 - Waste drainage layout
 - Demoilshed
 - Rainwater layout

Proposed Materials:
Ground Floor Walls: Render Walls to match existing
Flat Roof: GRP or single ply membrane
All new drainage to match materials of existing drainage

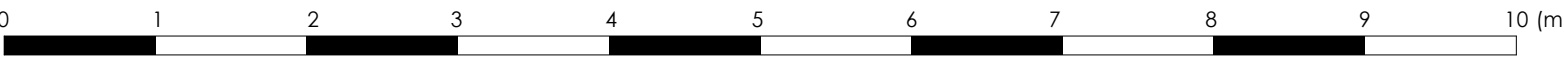

Note to Contractor: Contractor is recommended to carry out an intrusive site investigation prior to commencing works on site to ensure all details designed for this project are appropriate. Contractor to cross reference with Structural Calculations package for suitability, to assess site levels and confirm any design assumptions within the calculations package prior to works commencing on site. If the Contractor requires any additional information, please send a Request For Information to hello@planituk.co.uk before ordering materials and starting the works - requests will be acknowledged and responded to as soon as possible. Please ensure that the drawings have been submitted to Building Control for a Full Plans submission and the compliance report has been discharged before starting works on site. All dimensions must be checked and verified on site by the contractor prior to the commencement of any works. Any discrepancies or variations must be reported to Plan It UK immediately. Do not scale from this drawing. Drain location is an estimated location, contractor to investigate on site and allow a time and cost contingency for adjustments to drainage if required.

Drawn by:
AR

Title Number:

Project:
26 Agaton Road, London, SE9 3RW

Date:
25.06.2026

No:
26-2089


Rev:
00

Page:
D09

Client:
Emma Chang

Drawing Title:
PROPOSED ROOF PLAN

Scale:
1:50 @A1, 1:100 @A3

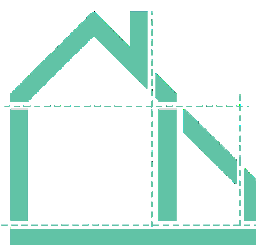


Plan It UK
Architectural Services
7 Leigh House, Bexleyheath, DA7 4QP
Enquiries@planituk.co.uk
Engineer: se@planituk.co.uk


EXISTING



Front Elevation

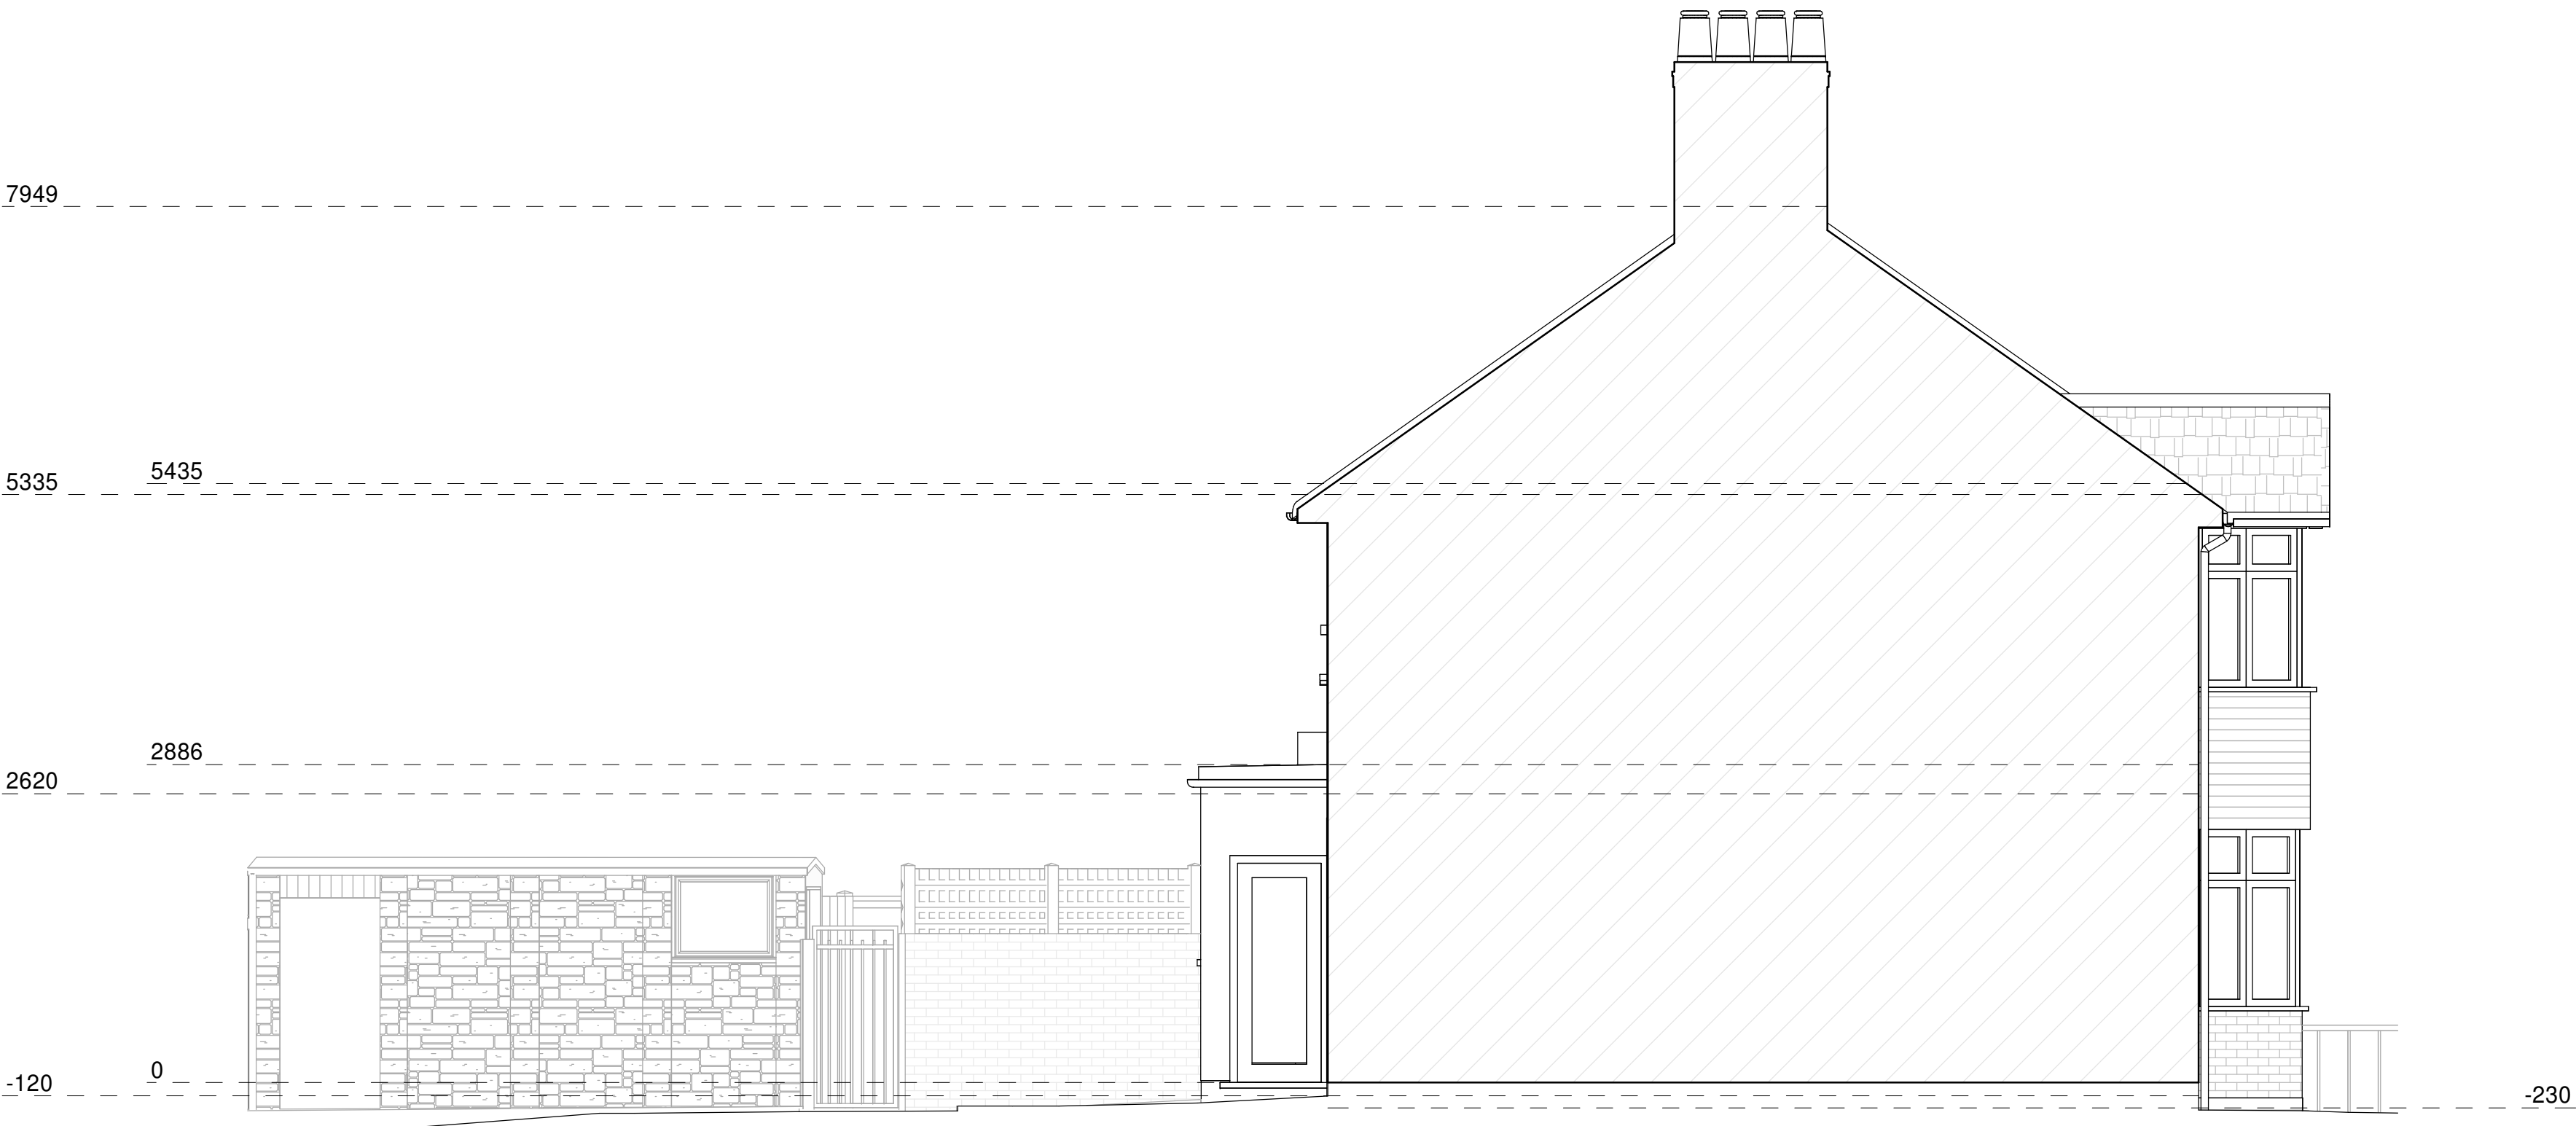

Left Side Elevation

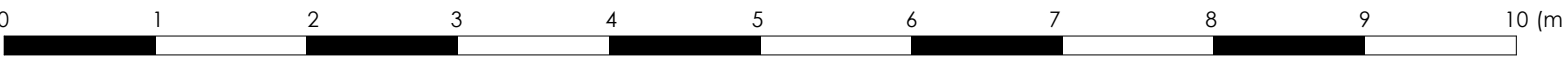


Note to Contractor: Contractor is recommended to carry out an intrusive site investigation prior to commencing works on site to ensure all details designed for this project are appropriate. Contractor to cross reference with Structural Calculations package for suitability, to assess site levels and confirm any design assumptions within the calculations package prior to works commencing on site. If the Contractor requires any additional information, please send a Request For Information to hello@planituk.co.uk before ordering materials and starting the works - requests will be acknowledged and responded to as soon as possible. Please ensure that the drawings have been submitted to Building Control for a Full Plans submission and the compliance report has been discharged before starting works on site. All dimensions must be checked and verified on site by the contractor prior to the commencement of any works. Any discrepancies or variations must be reported to Plan It UK immediately. Do not scale from this drawing. Drain location is an estimated location, contractor to investigate on site and allow a time and cost contingency for adjustments to drainage if required.

Drawn by: AR	Title Number:	Project: 26 Agaton Road, London, SE9 3RW	Date: 25.06.2026	No: 26-2089	Plan It UK Architectural Services 7 Leigh House, Bexleyheath, DA7 4QP Enquiries@planituk.co.uk Engineer: se@planituk.co.uk
Client: Emma Chang		Drawing Title: EXISTING FRONT AND LEFT ELEVATIONS	Scale: 1:50 @A1, 1:100 @A3	Rev: 00	
				Page: D10	

PROPOSED



Front Elevation

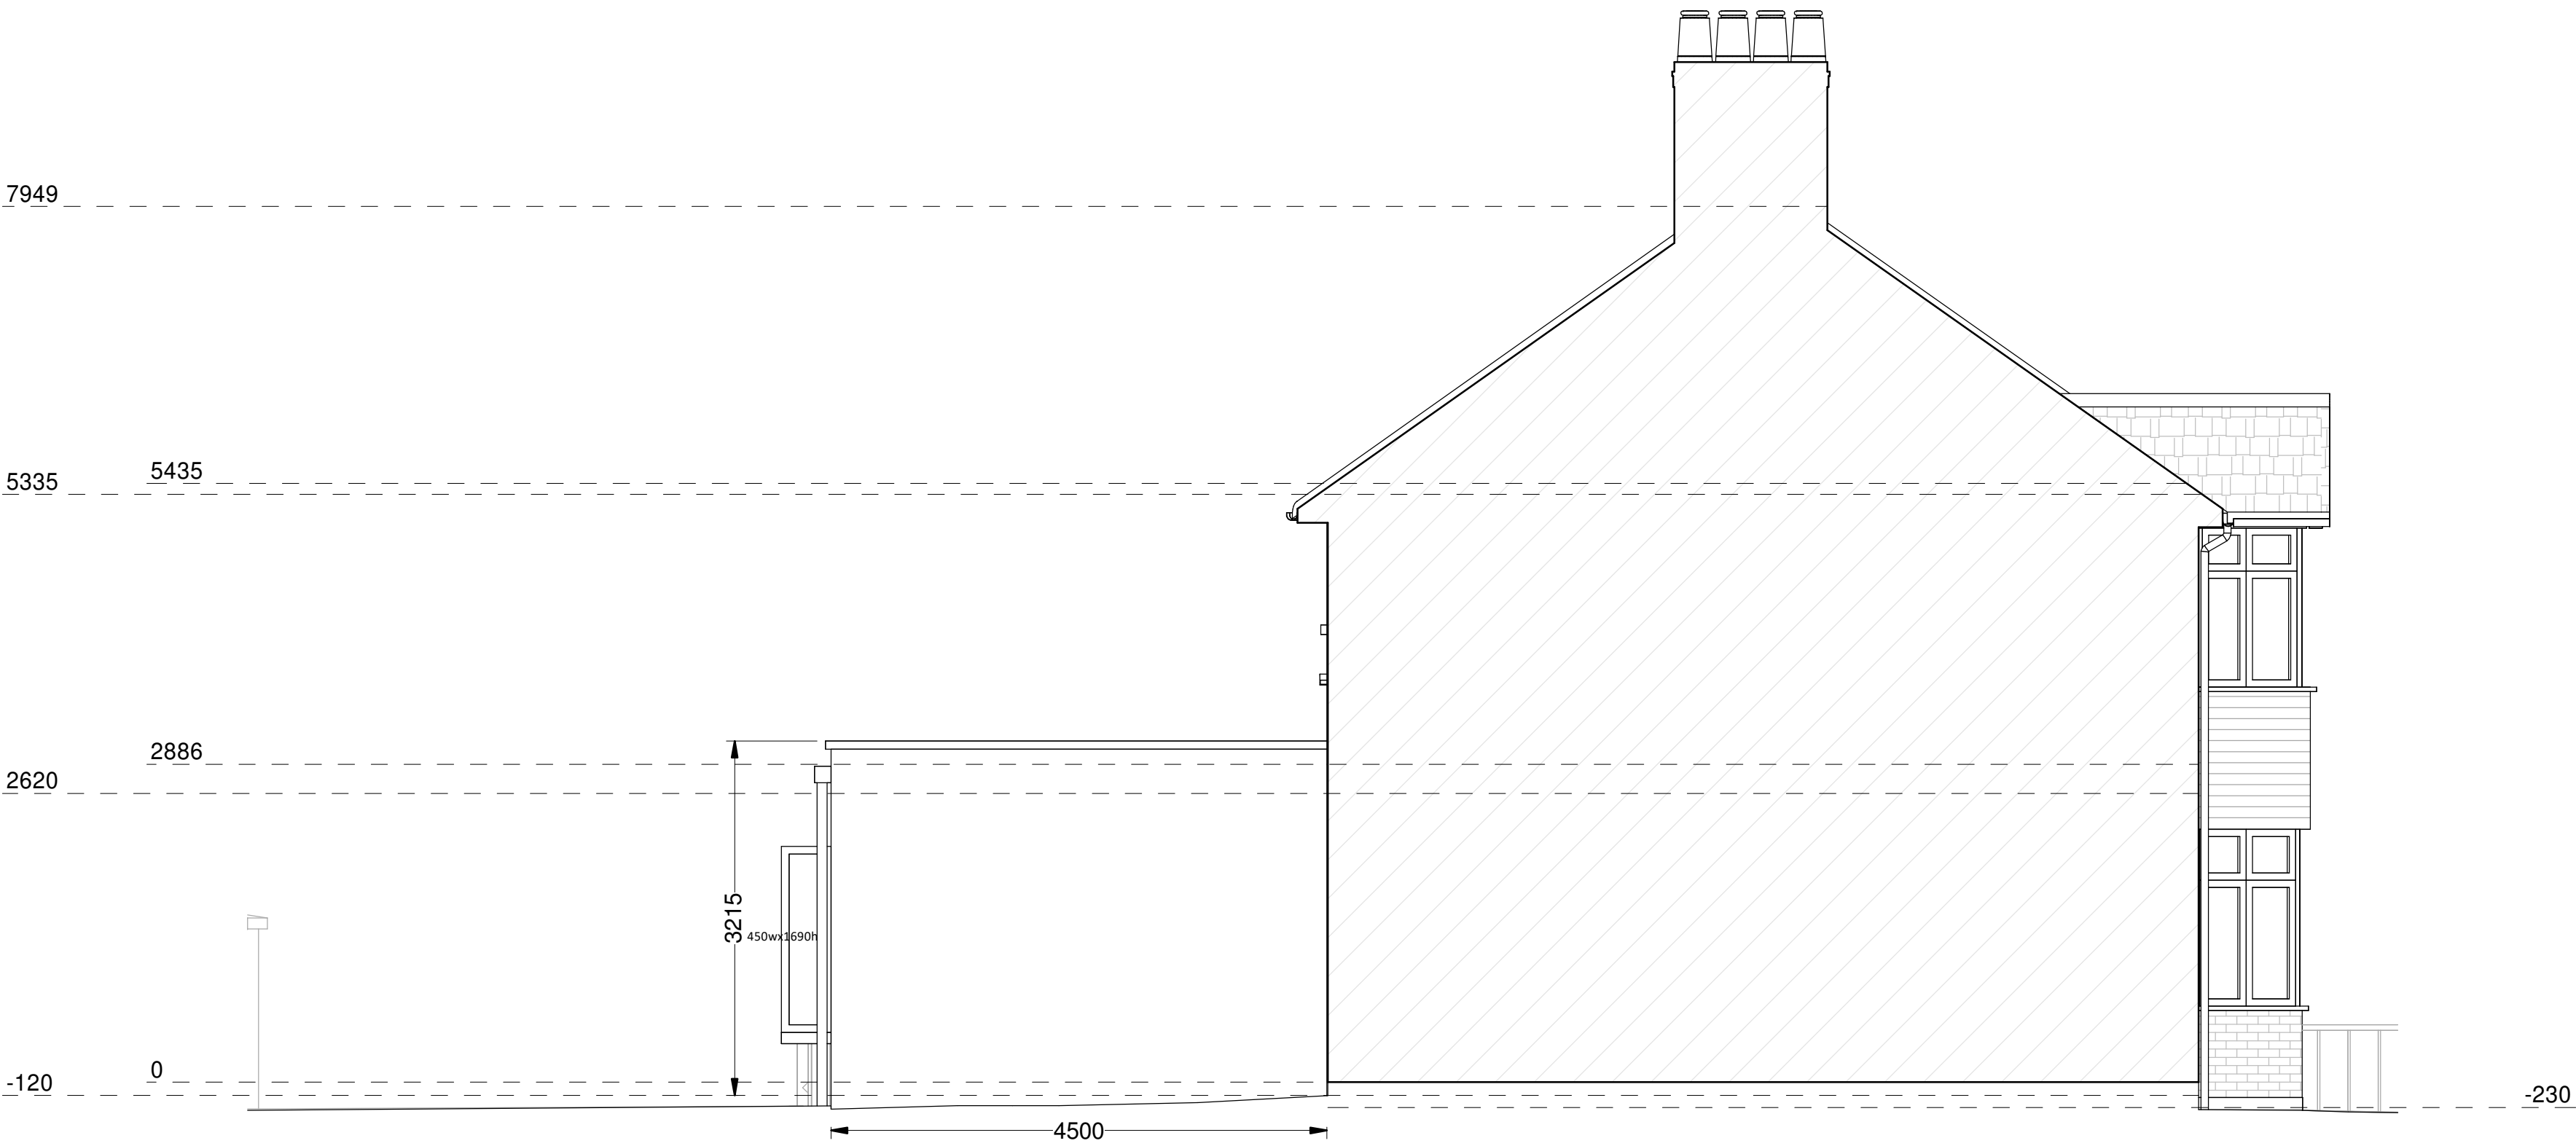


Left Side Elevation

Symbol Key

- Proposed wall
- Boundary Line
- Details above
- Waste drainage layout
- Demoilshed
- Rainwater layout

Proposed Materials:
Ground Floor Walls: Render Walls to match existing
Flat Roof: GRP or single ply membrane
All new drainage to match materials of existing drainage

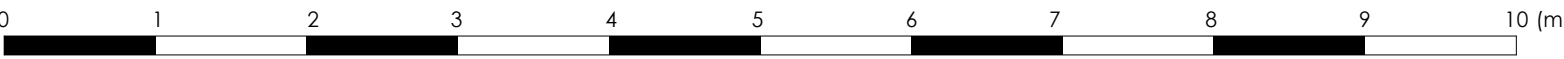

Note to Contractor: Contractor is recommended to carry out an intrusive site investigation prior to commencing works on site to ensure all details designed for this project are appropriate. Contractor to cross reference with Structural Calculations package for suitability, to assess site levels and confirm any design assumptions within the calculations package prior to works commencing on site. If the Contractor requires any additional information, please send a Request For Information to hello@planituk.co.uk before ordering materials and starting the works - requests will be acknowledged and responded to as soon as possible. Please ensure that the drawings have been submitted to Building Control for a Full Plans submission and the compliance report has been discharged before starting works on site. All dimensions must be checked and verified on site by the contractor prior to the commencement of any works. Any discrepancies or variations must be reported to Plan It UK immediately. Do not scale from this drawing. Drain location is an estimated location, contractor to investigate on site and allow a time and cost contingency for adjustments to drainage if required.

Drawn by:
AR

Title Number:

Project:
26 Agaton Road, London, SE9 3RW

Date:
25.06.2026

No:
26-2089

Rev:
00

Page:
D11



7 Leigh House, Bexleyheath, DA7 4QP

Enquiries@planituk.co.uk

Engineer: se@planituk.co.uk

Client:
Emma Chang

Drawing Title:
PROPOSED FRONT AND LEFT ELEVATIONS

Scale:
1:50 @A1, 1:100 @A3

EXISTING



Rear Elevation



Right Side Elevation

Note to Contractor: Contractor is recommended to carry out an intrusive site investigation prior to commencing works on site to ensure all details designed for this project are appropriate. Contractor to cross reference with Structural Calculations package for suitability, to assess site levels and confirm any design assumptions within the calculations package prior to works commencing on site. If the Contractor requires any additional information, please send a Request For Information to hello@planituk.co.uk before ordering materials and starting the works - requests will be acknowledged and responded to as soon as possible. Please ensure that the drawings have been submitted to Building Control for a Full Plans submission and the compliance report has been discharged before starting works on site. All dimensions must be checked and verified on site by the contractor prior to the commencement of any works. Any discrepancies or variations must be reported to Plan It UK immediately. Do not scale from this drawing. Drain location is an estimated location, contractor to investigate on site and allow a time and cost contingency for adjustments to drainage if required.

Drawn by:
AR

Title Number:

Project:
26 Agaton Road, London, SE9 3RW

Date:
25.06.2026

No:
26-2089


Client:
Emma Chang

Drawing Title:
EXISTING REAR AND RIGHT ELEVATIONS

Scale:
1:50 @A1, 1:100 @A3

Rev:
00

Page:
D12

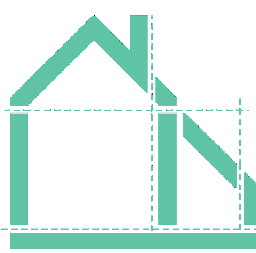

Plan It UK

Architectural Services

7 Leigh House, Bexleyheath, DA7 4QP

Enquiries@planituk.co.uk

Engineer: se@planituk.co.uk

PROPOSED



Rear Elevation




Right Side Elevation

Symbol Key

- Proposed wall
- Boundary Line
- Details above
- Waste drainage layout
- Demoilshed
- Rainwater layout

Proposed Materials:
Ground Floor Walls: Render Walls to match existing
Flat Roof: GRP or single ply membrane
All new drainage to match materials of existing drainage

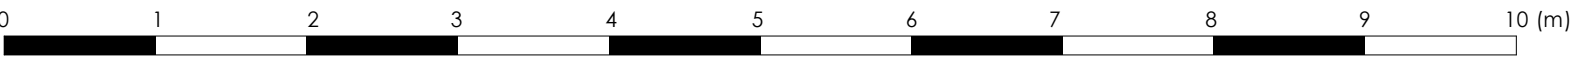

Note to Contractor: Contractor is recommended to carry out an intrusive site investigation prior to commencing works on site to ensure all details designed for this project are appropriate. Contractor to cross reference with Structural Calculations package for suitability, to assess site levels and confirm any design assumptions within the calculations package prior to works commencing on site. If the Contractor requires any additional information, please send a Request For Information to hello@planituk.co.uk before ordering materials and starting the works - requests will be acknowledged and responded to as soon as possible. Please ensure that the drawings have been submitted to Building Control for a Full Plans submission and the compliance report has been discharged before starting works on site. All dimensions must be checked and verified on site by the contractor prior to the commencement of any works. Any discrepancies or variations must be reported to Plan It UK immediately. Do not scale from this drawing. Drain location is an estimated location, contractor to investigate on site and allow a time and cost contingency for adjustments to drainage if required.

Drawn by:
AR

Title Number:

Project:
26 Agaton Road, London, SE9 3RW

Date:
25.06.2026

No:
26-2089


Rev:
00

Page:
D13

Client:
Emma Chang

Drawing Title:
PROPOSED REAR AND RIGHT ELEVATIONS

Scale:
1:50 @A1, 1:100 @A3

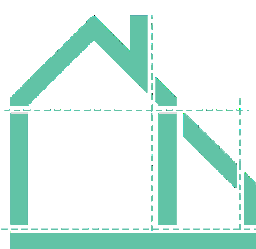

Plan It UK


Architectural Services

7 Leigh House, Bexleyheath, DA7 4QP

Enquiries@planituk.co.uk

Engineer: se@planituk.co.uk


PROPOSED

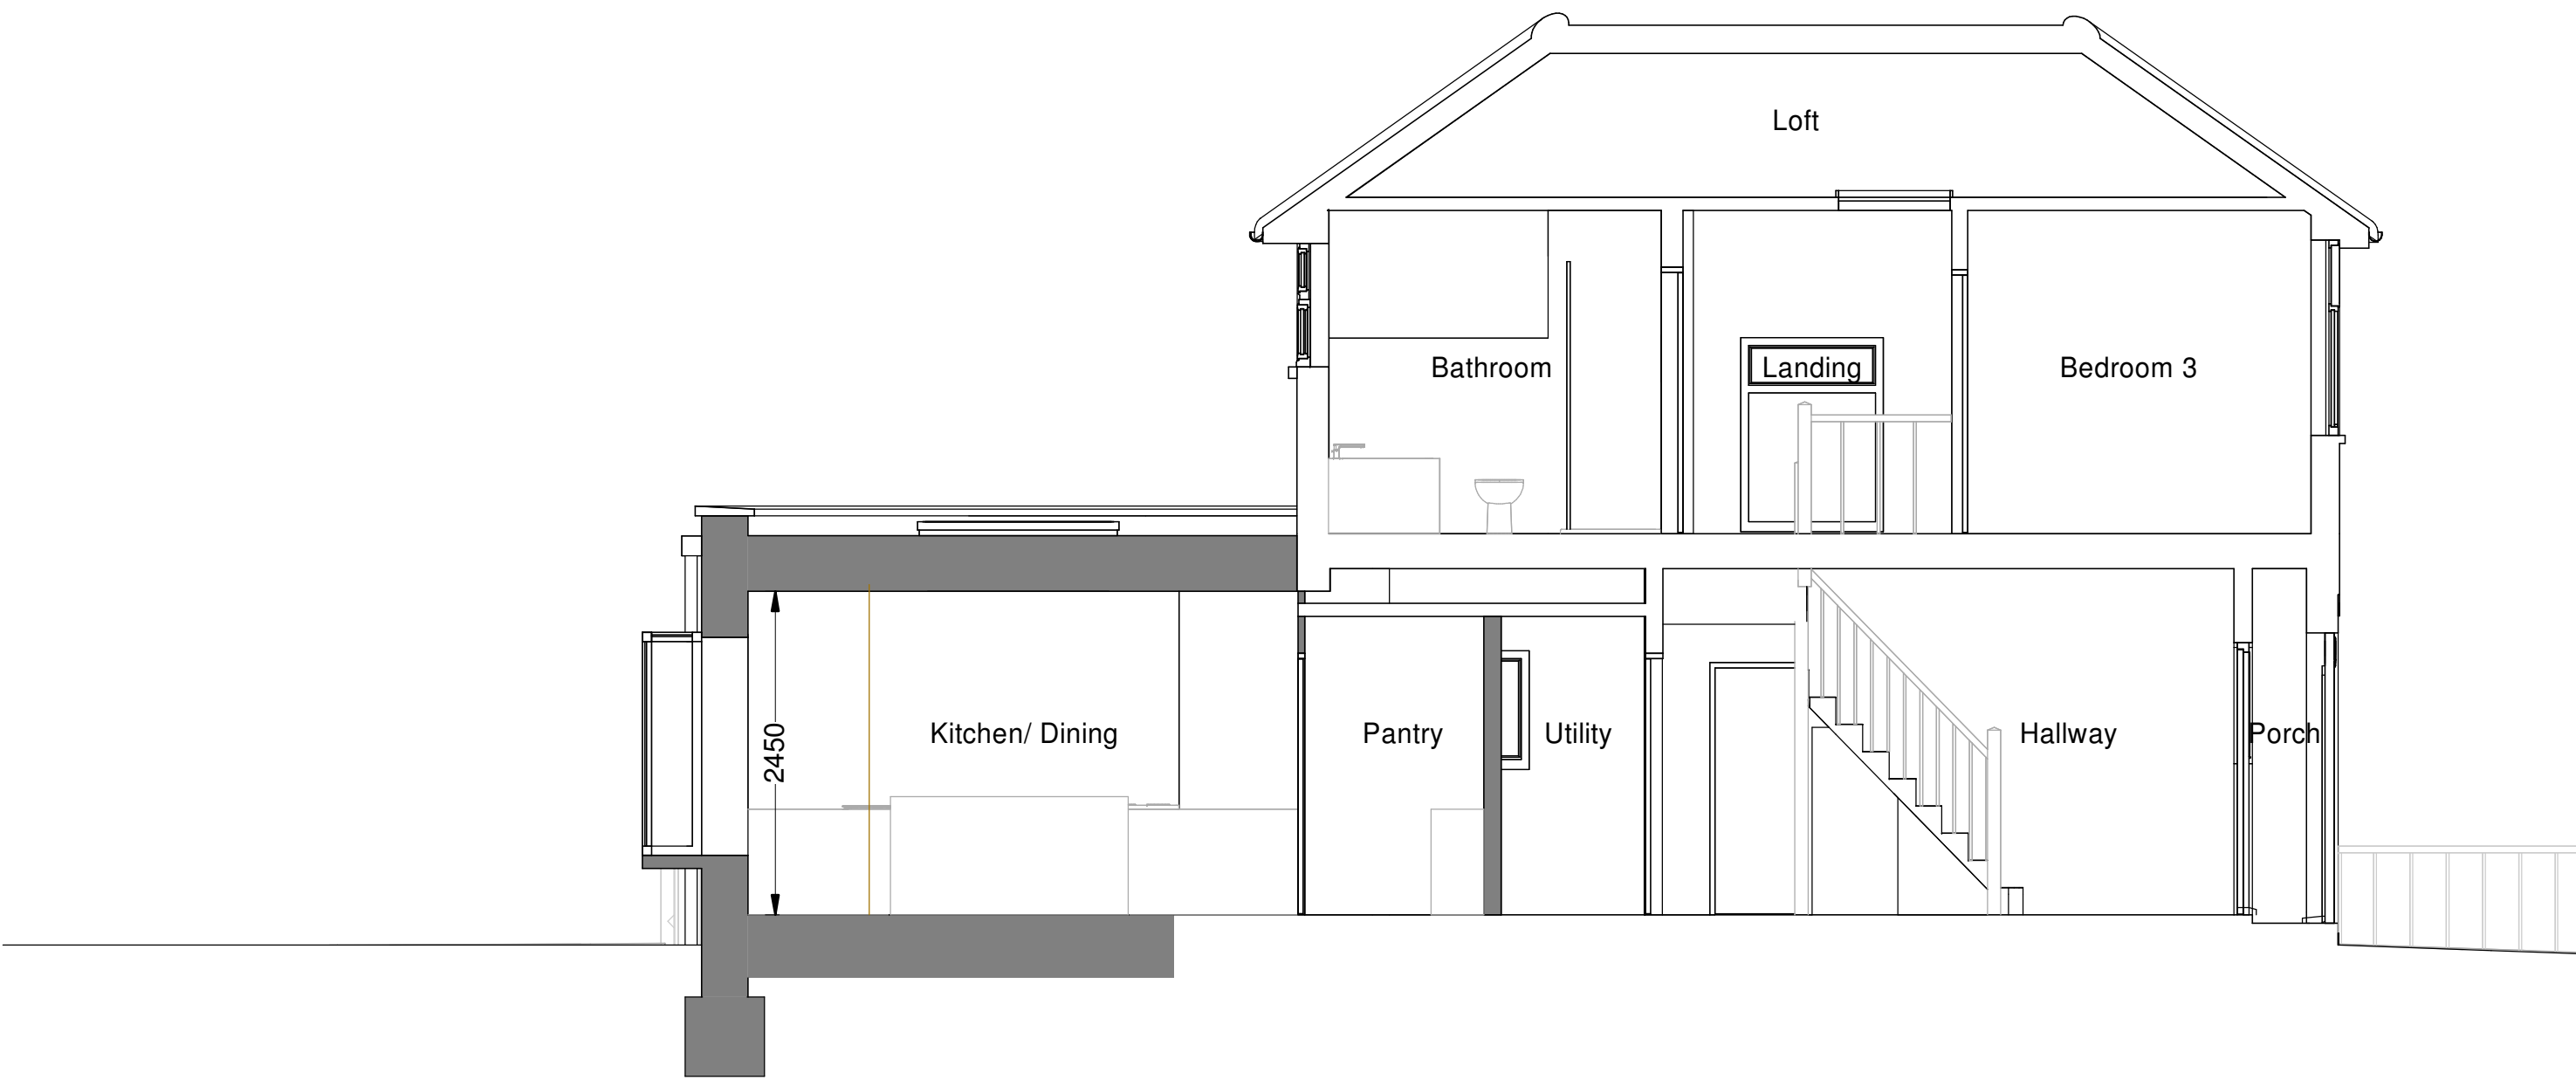

Section A - A

- Symbol Key
- Proposed wall
 - Boundary Line
 - Details above
 - Waste drainage layout
 - Demolished
 - Rainwater layout


Proposed Materials:
Ground Floor Walls: Render Walls to match existing
Flat Roof: GRP or single ply membrane
All new drainage to match materials of existing drainage

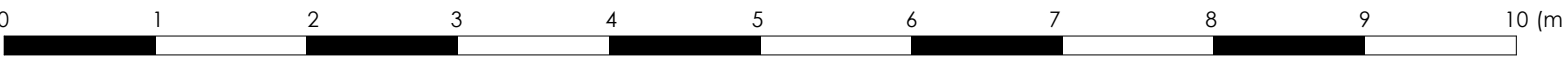


Note to Contractor: Contractor is recommended to carry out an intrusive site investigation prior to commencing works on site to ensure all details designed for this project are appropriate. Contractor to cross reference with Structural Calculations package for suitability, to assess site levels and confirm any design assumptions within the calculations package prior to works commencing on site. If the Contractor requires any additional information, please send a Request For Information to hello@planituk.co.uk before ordering materials and starting the works - requests will be acknowledged and responded to as soon as possible. Please ensure that the drawings have been submitted to Building Control for a Full Plans submission and the compliance report has been discharged before starting works on site. All dimensions must be checked and verified on site by the contractor prior to the commencement of any works. Any discrepancies or variations must be reported to Plan It UK immediately. Do not scale from this drawing. Drain location is an estimated location, contractor to investigate on site and allow a time and cost contingency for adjustments to drainage if required.

Drawn by: AR	Title Number:	Project: 26 Agaton Road, London, SE9 3RW	Date: 25.06.2026	No: 26-2089	Plan It UK Architectural Services 7 Leigh House, Bexleyheath, DA7 4QP Enquiries@planituk.co.uk Engineer: se@planituk.co.uk
Client: Emma Chang		Drawing Title: PROPOSED SECTION	Scale: 1:50 @A1, 1:100 @A3	Rev: 00	
				Page: D14	


EXISTING

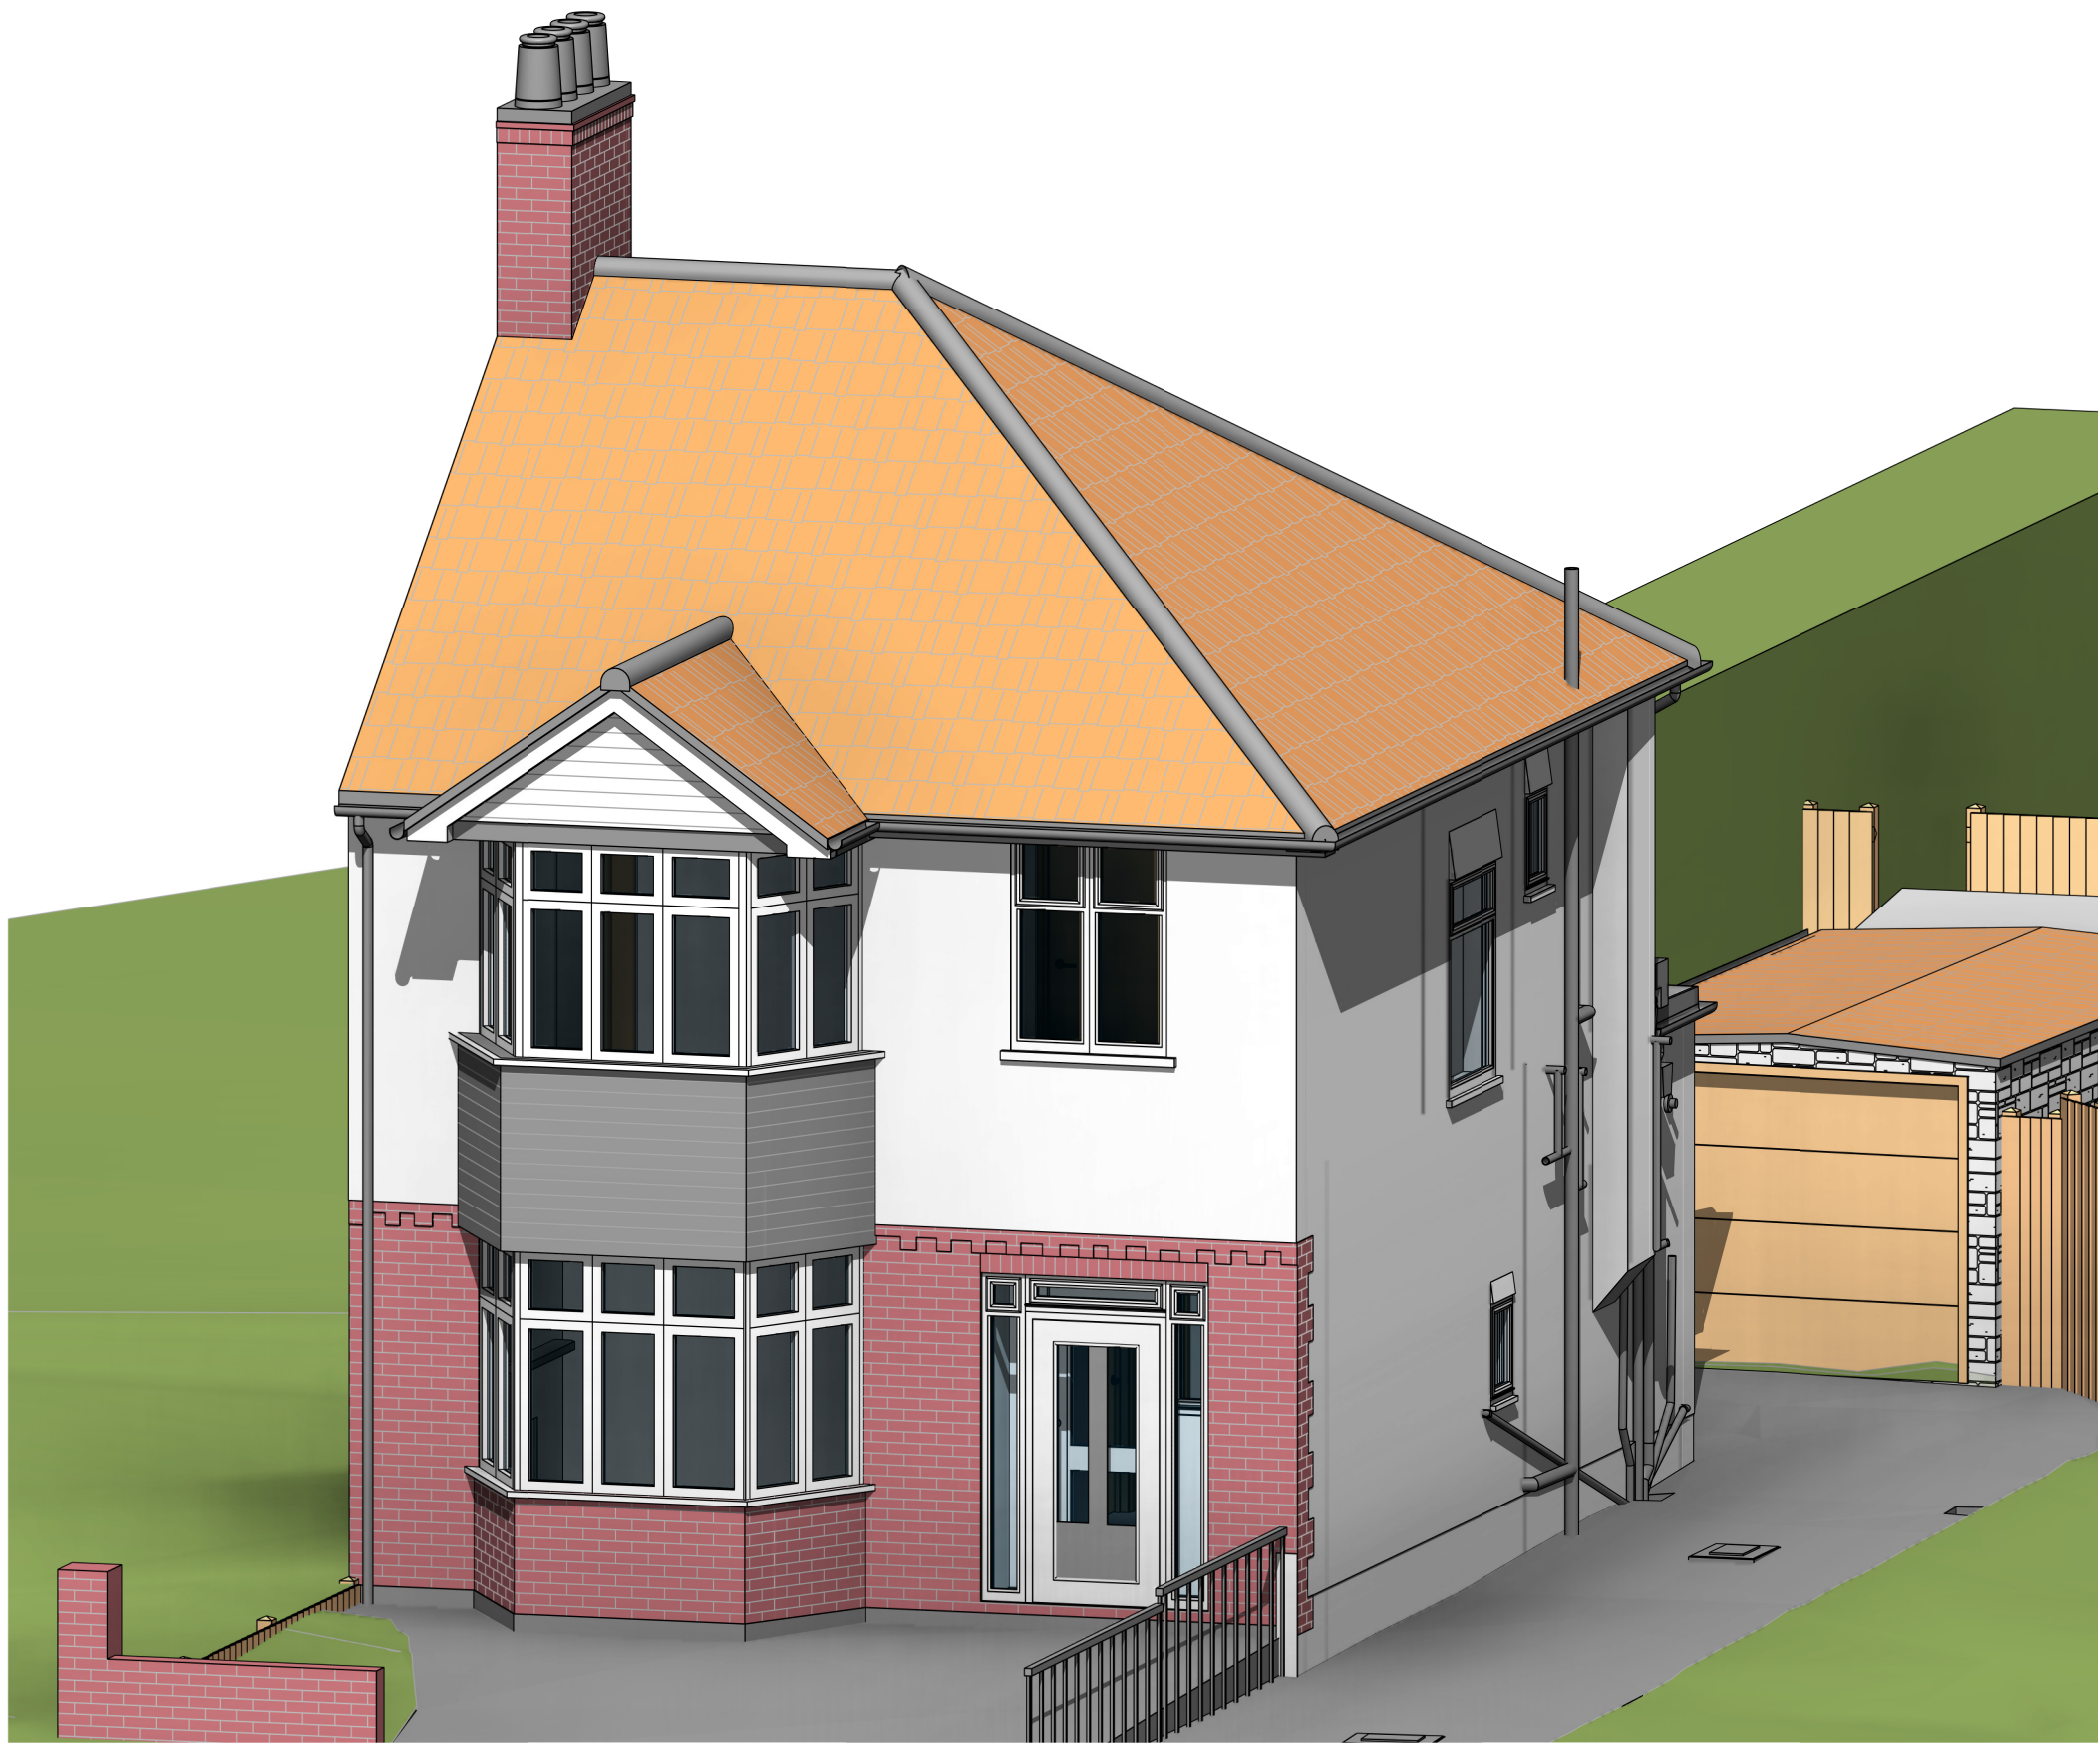

3D Front View

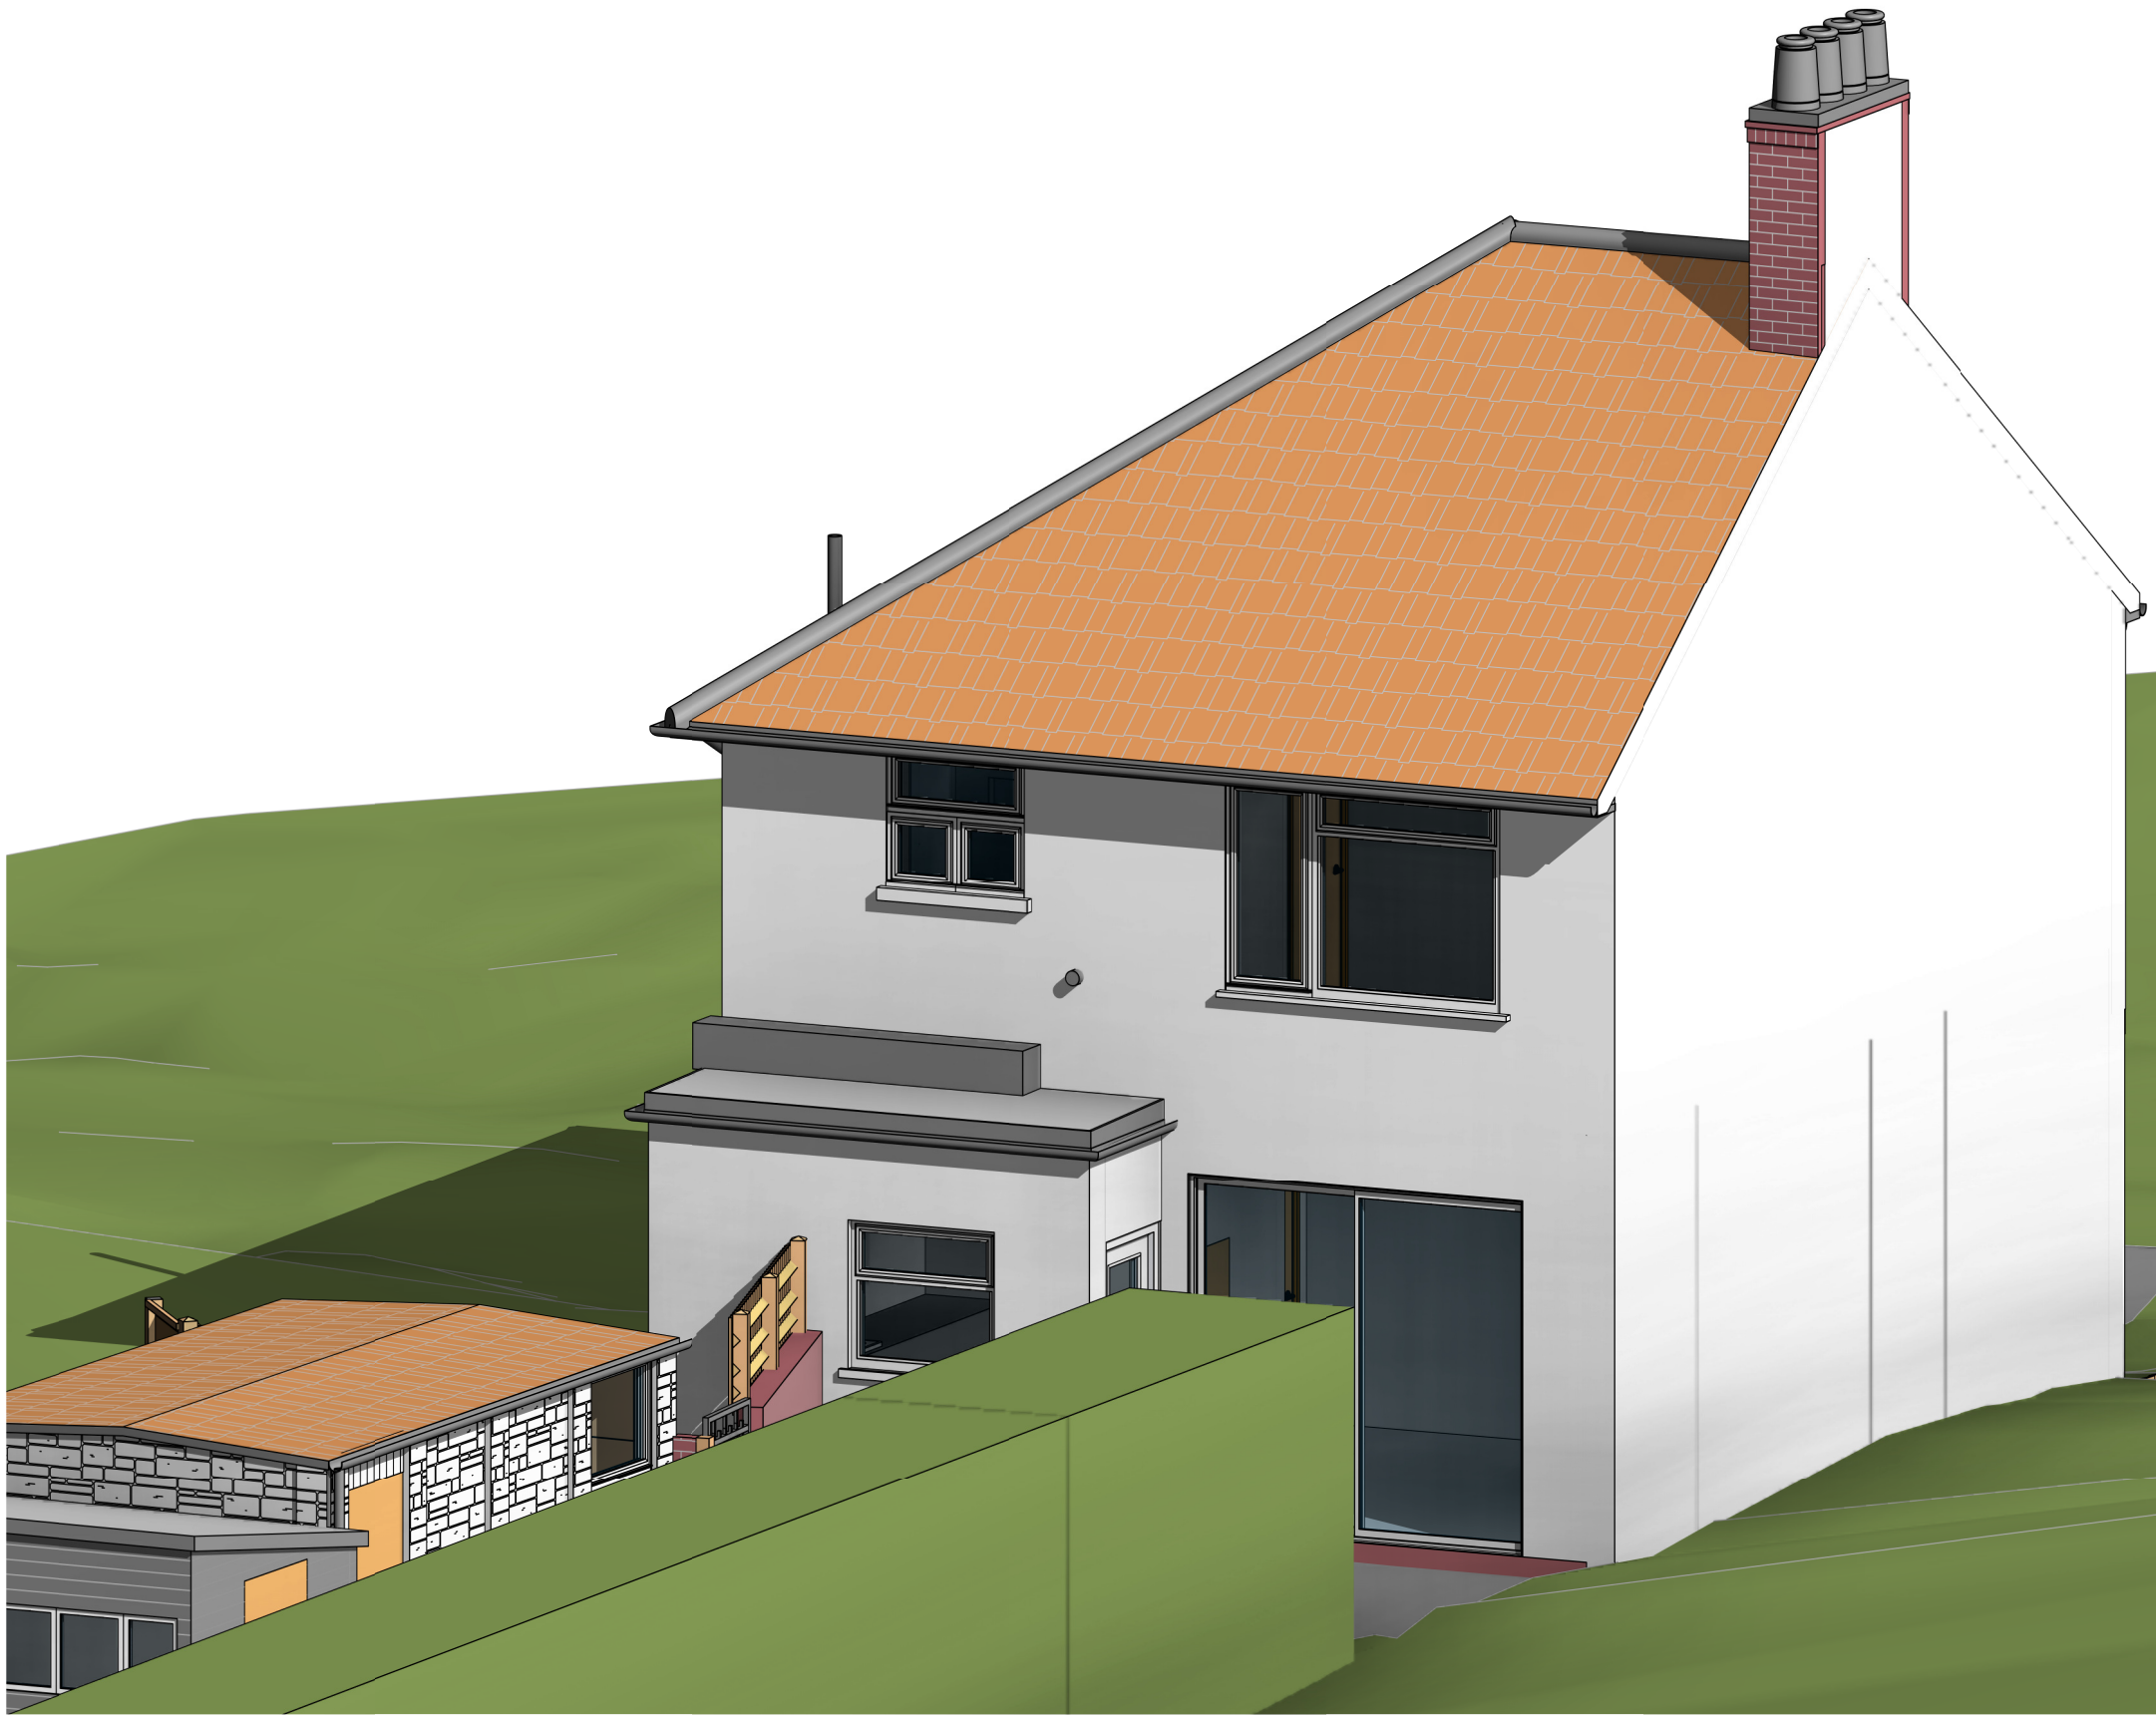

3D Rear View

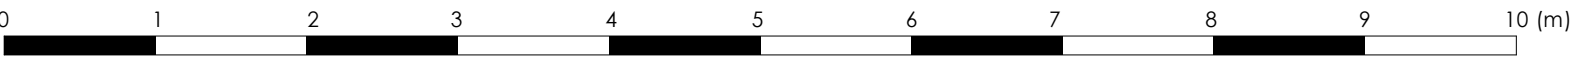


Note to Contractor: Contractor is recommended to carry out an intrusive site investigation prior to commencing works on site to ensure all details designed for this project are appropriate. Contractor to cross reference with Structural Calculations package for suitability, to assess site levels and confirm any design assumptions within the calculations package prior to works commencing on site. If the Contractor requires any additional information, please send a Request For Information to hello@planituk.co.uk before ordering materials and starting the works - requests will be acknowledged and responded to as soon as possible. Please ensure that the drawings have been submitted to Building Control for a Full Plans submission and the compliance report has been discharged before starting works on site. All dimensions must be checked and verified on site by the contractor prior to the commencement of any works. Any discrepancies or variations must be reported to Plan It UK immediately. Do not scale from this drawing. Drain location is an estimated location, contractor to investigate on site and allow a time and cost contingency for adjustments to drainage if required.

Drawn by: AR	Title Number:	Project: 26 Agaton Road, London, SE9 3RW	Date: 25.06.2026	No: 26-2089	 7 Leigh House, Bexleyheath, DA7 4QP Enquiries@planituk.co.uk Engineer: se@planituk.co.uk
Client: Emma Chang		Drawing Title: EXISTING 3D VIEWS	Scale: 1:50 @A1, 1:100 @A3	Rev: 00	
				Page: D15	


PROPOSED



3D Front View

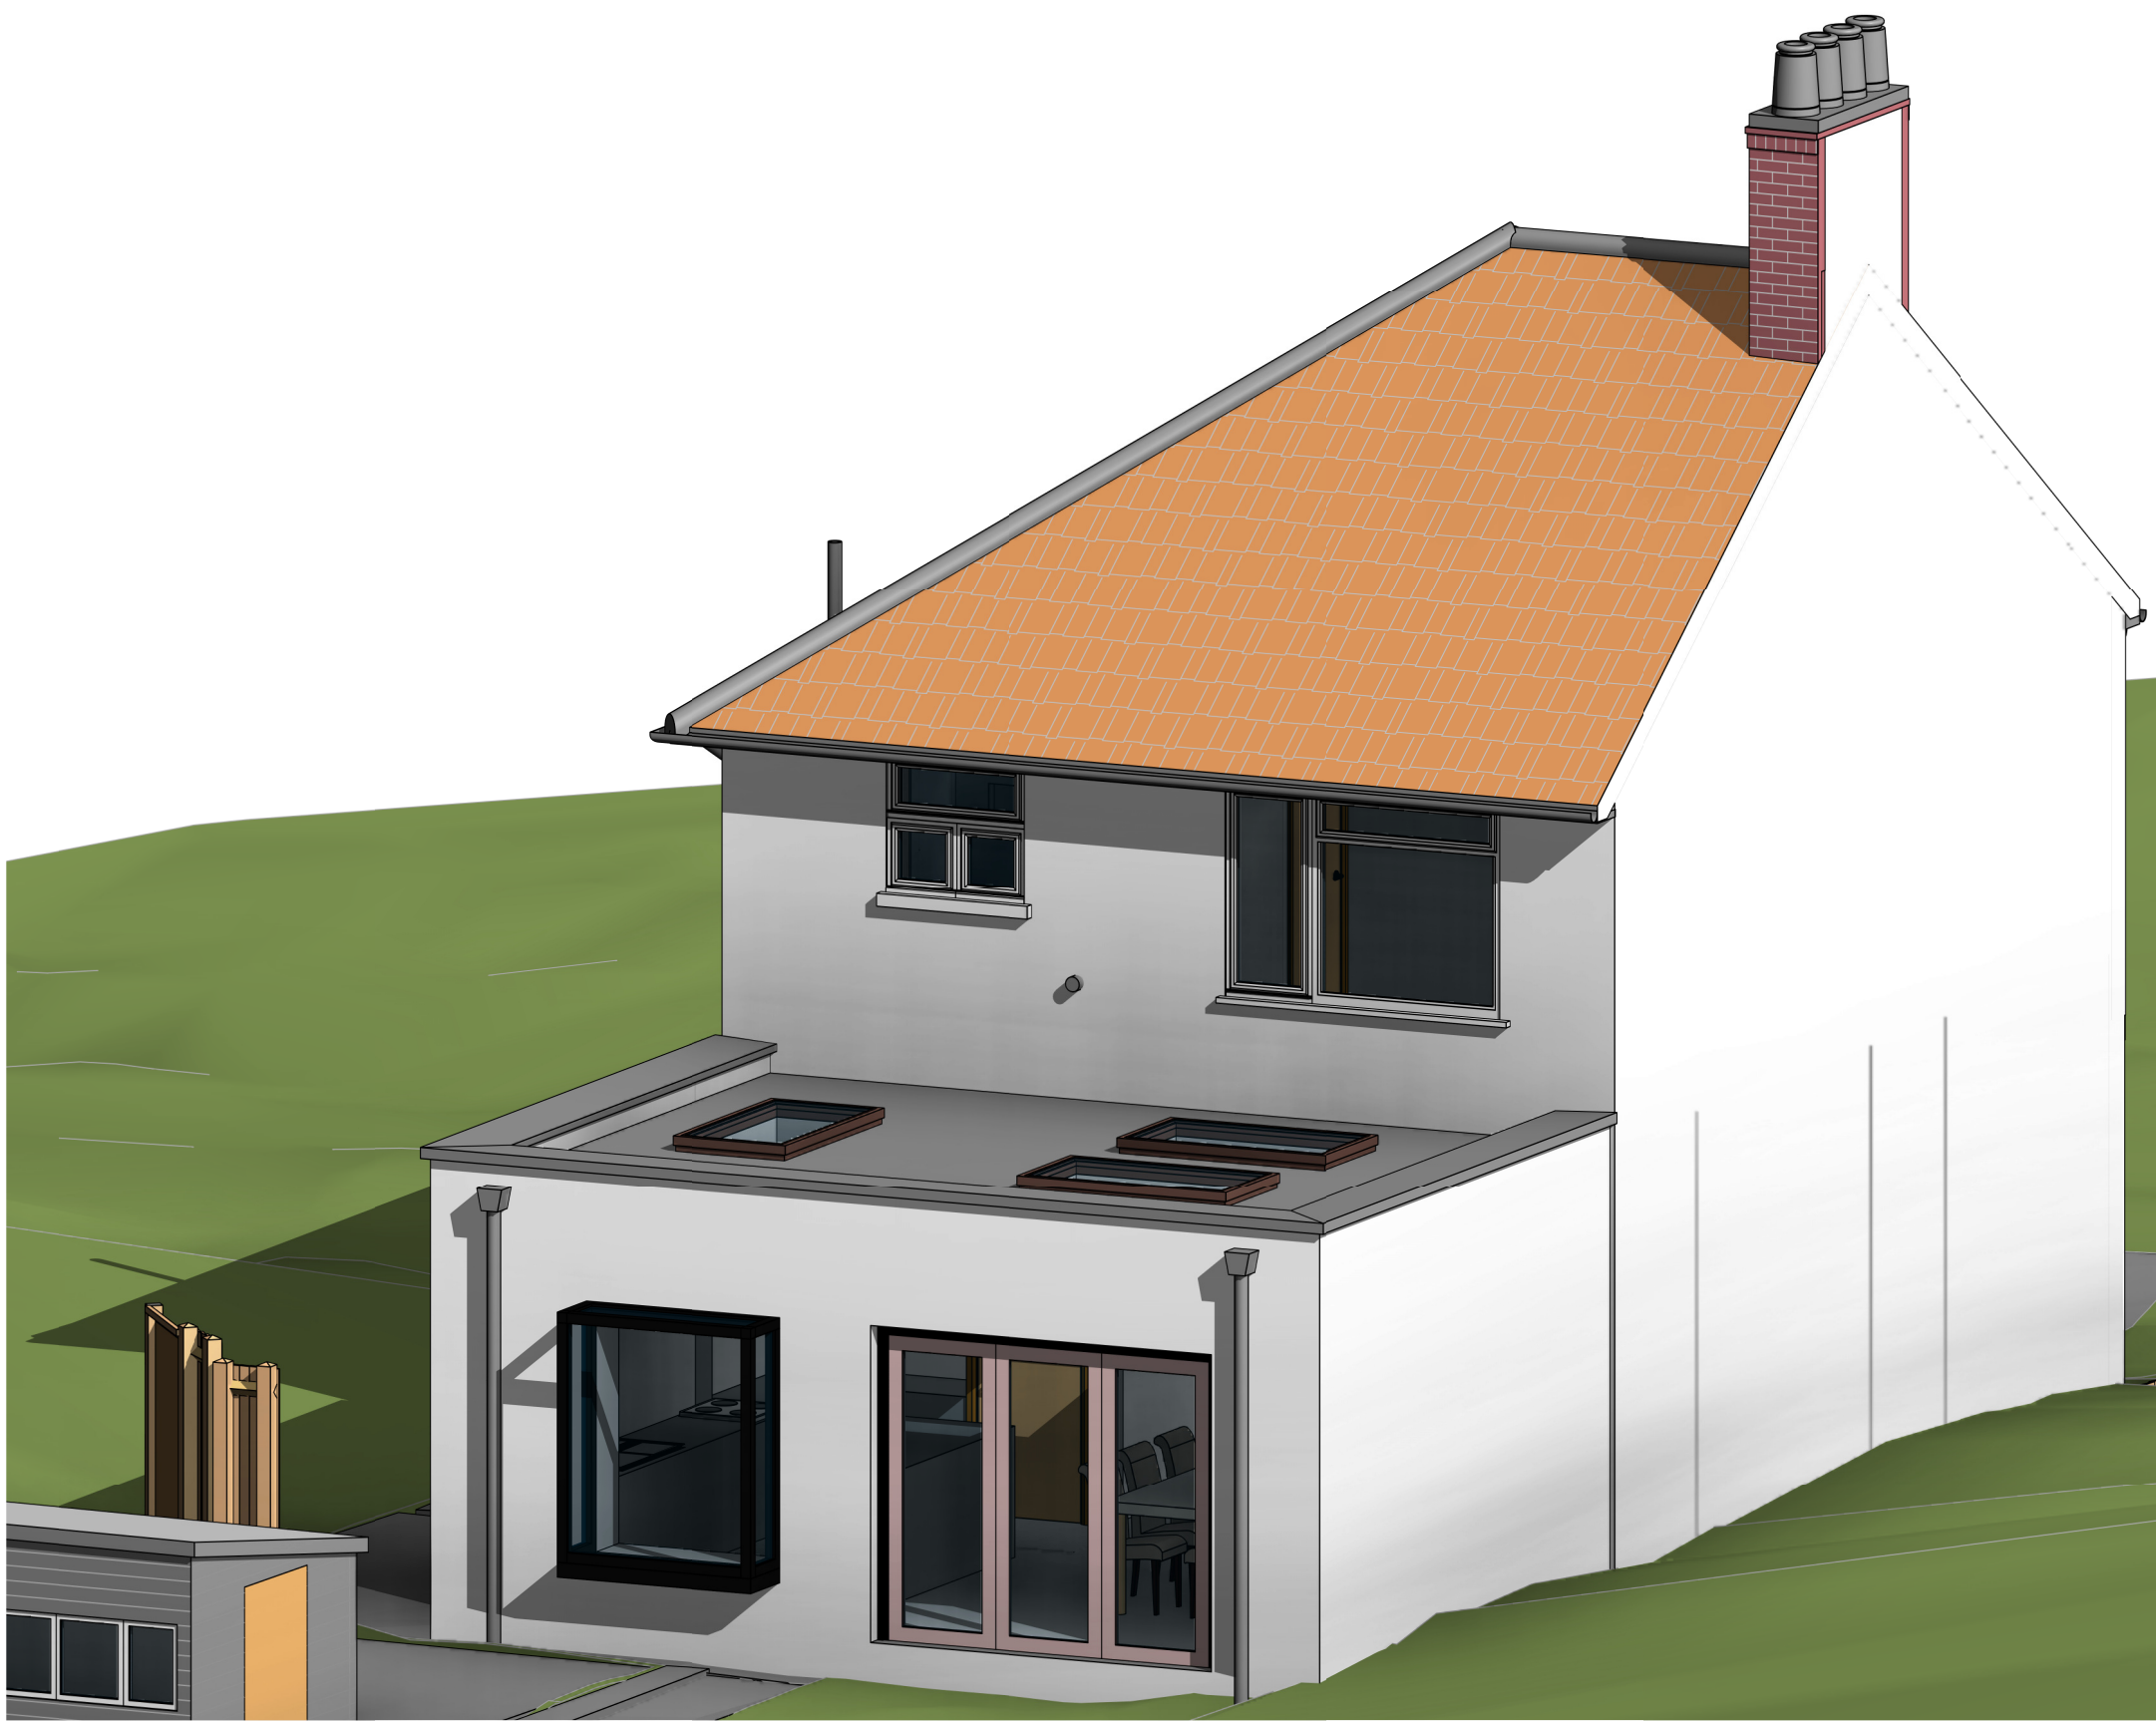

3D Rear View

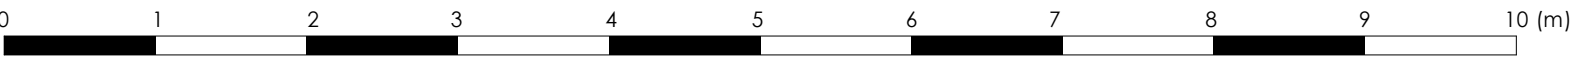

Note to Contractor: Contractor is recommended to carry out an intrusive site investigation prior to commencing works on site to ensure all details designed for this project are appropriate. Contractor to cross reference with Structural Calculations package for suitability, to assess site levels and confirm any design assumptions within the calculations package prior to works commencing on site. If the Contractor requires any additional information, please send a Request For Information to hello@planituk.co.uk before ordering materials and starting the works - requests will be acknowledged and responded to as soon as possible. Please ensure that the drawings have been submitted to Building Control for a Full Plans submission and the compliance report has been discharged before starting works on site. All dimensions must be checked and verified on site by the contractor prior to the commencement of any works. Any discrepancies or variations must be reported to Plan It UK immediately. Do not scale from this drawing. Drain location is an estimated location, contractor to investigate on site and allow a time and cost contingency for adjustments to drainage if required.

Drawn by: AR	Title Number:	Project: 26 Agaton Road, London, SE9 3RW	Date: 25.06.2026	No: 26-2089	 7 Leigh House, Bexleyheath, DA7 4QP Enquiries@planituk.co.uk Engineer: se@planituk.co.uk
Client: Emma Chang		Drawing Title: PROPOSED 3D VIEWS	Scale: 1:50 @A1, 1:100 @A3	Rev: 00	
				Page: D16	